

ФАСАД

двери закрыты

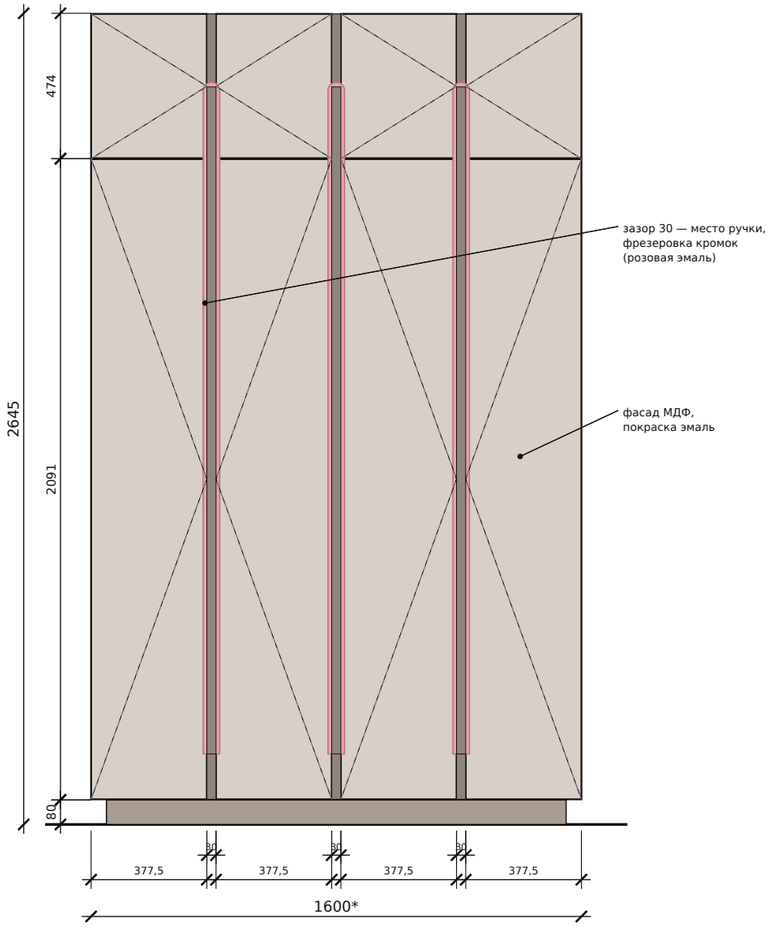


НАПОЛНЕНИЕ

фасады условно сняты

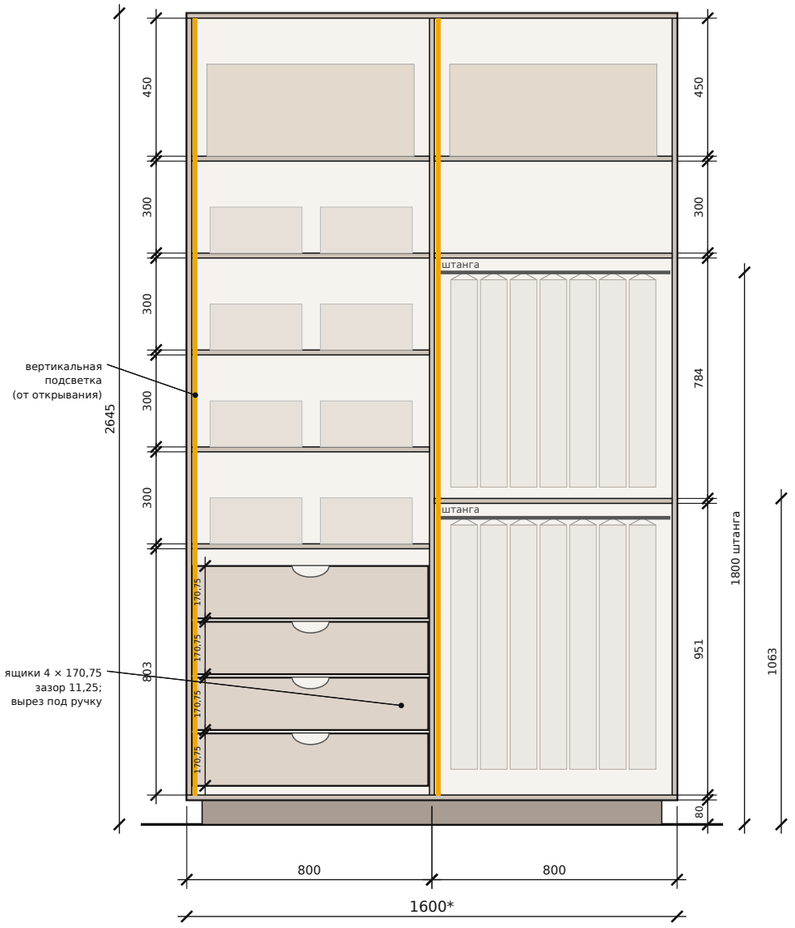


РАЗРЕЗ 1–1

по отсеку с ящиками

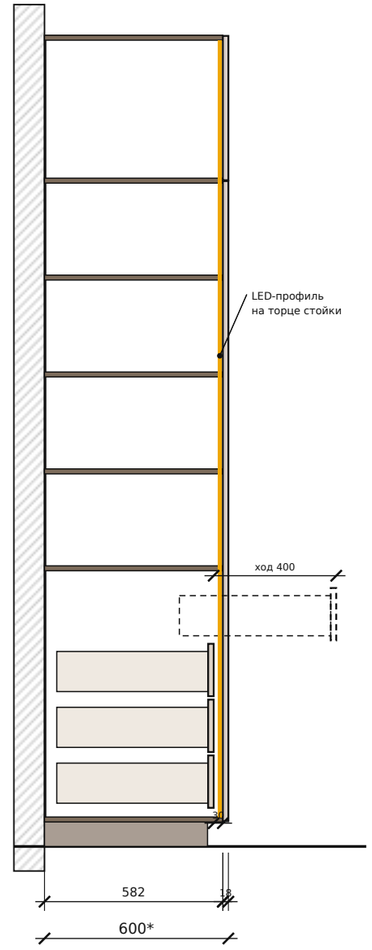

ПЛАН

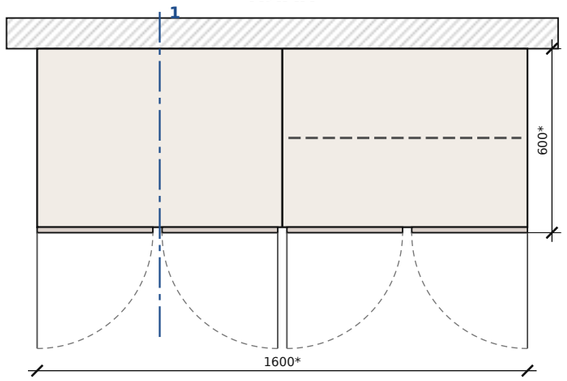

ПРИМЕЧАНИЯ

Корпус — ЛДСП Egger 16 мм, цвет «Кашемир»; цоколь 80.

Фасады — МДФ 18 мм, эмаль; 4 нижние + 4 антресольные двери по 377,5 мм.

Между фасадами на стыках зазор 30 — место ручки; кромки фрезерованы, розовая эмаль.

Левый отсек: антресоль 450, 4 полки с шагом 300, блок ящиков 803:
4 внутренних ящика, фасады 170,75, зазор 11,25, отступ 30 от края,
вырез под ручку, направляющие полного выдвижения 500 мм.

Правый отсек: антресоль 450, полка 300, штанга H=1800 (зона 784),
полка, нижняя штанга H=1000 (зона 951).

Вертикальная LED-подсветка в каждом отсеке, включение от открывания.

* Ширина 1600 и глубина 600 на эскизе не указаны — ПРИНЯТЫ, уточнить.

Размеры в свету между полками — как на эскизе заказчика.

ШКАФ С ЯЩИКАМИ

распашной, по эскизу заказчика

1600* × 600* × 2645 мм

ЛДСП Egger «Кашемир», МДФ эмаль

Размеры в мм

Масштаб **1:20**

Лист 1 (А3)