
Металлический каркас домика — план (вид сверху)

Труба профильная 80×80 | Домик на сваях | Высота 3000 | Шаг стоек ≤ 2000 | Под перегородками — только нижняя обвязка | Размеры в мм, 1:50

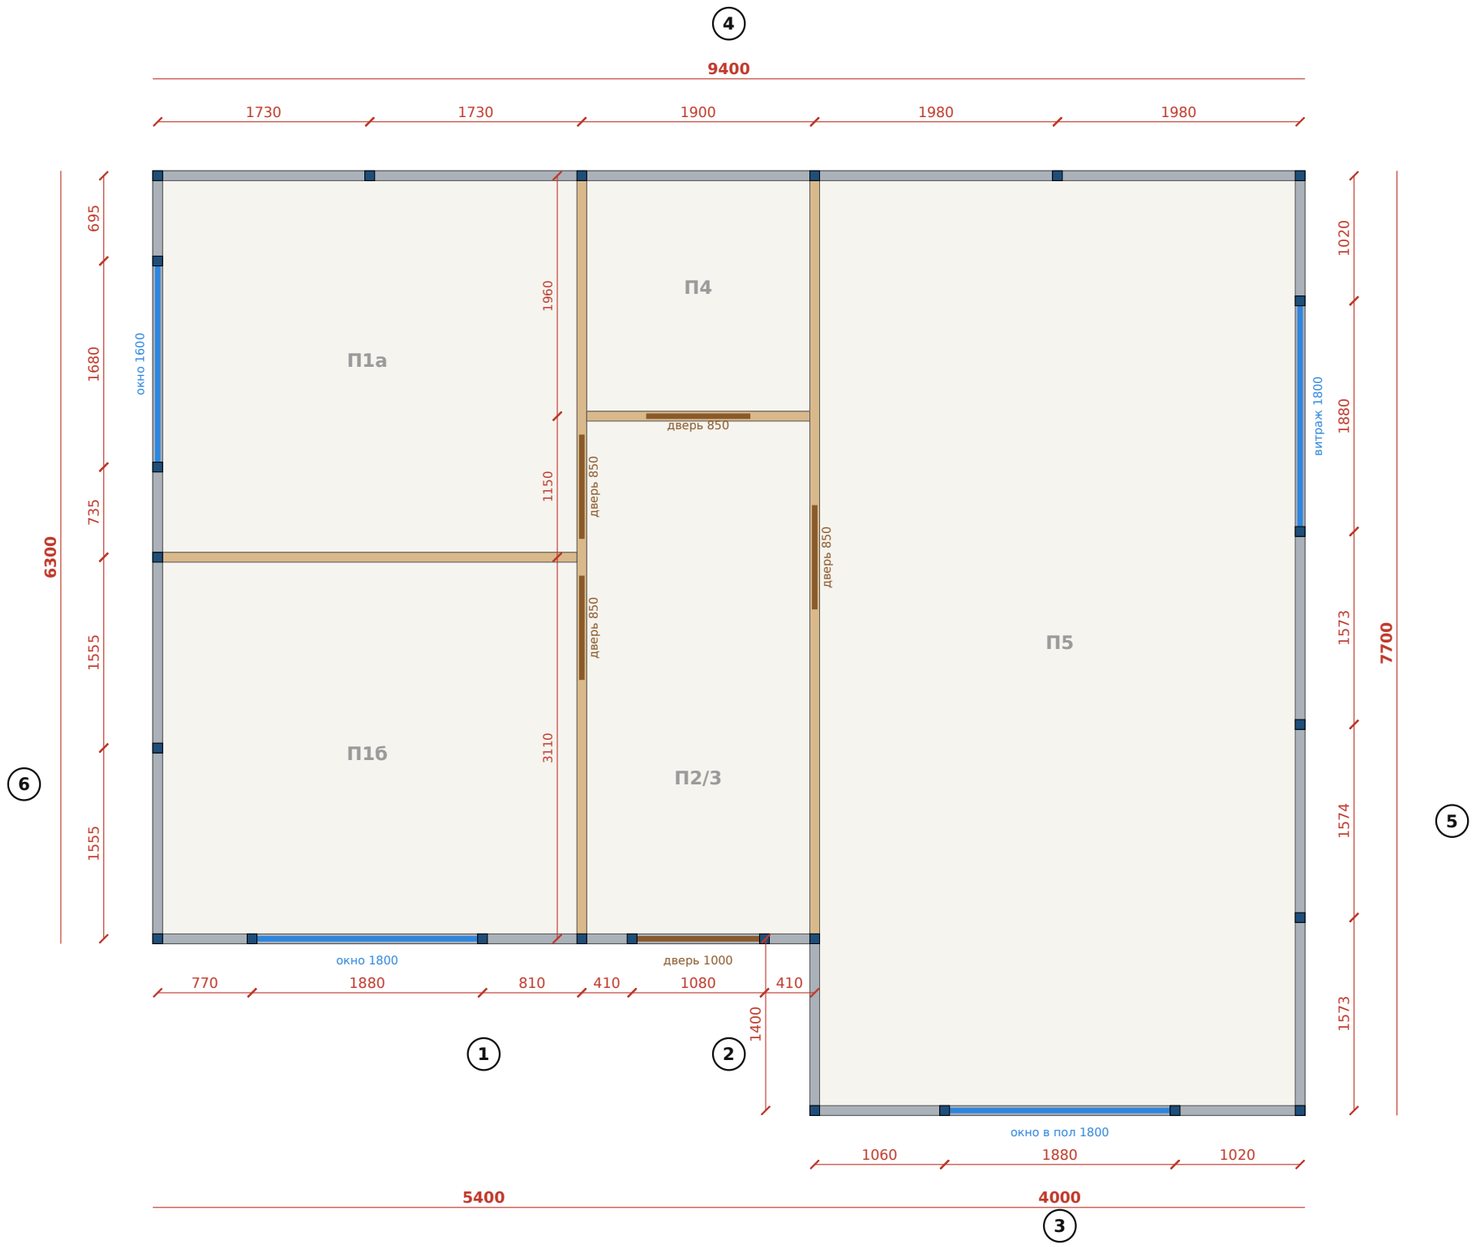

Условные обозначения

- Стойка 80×80, h = 2840 (между обвязками)
- Обвязка наружных стен (верхняя; нижняя — под ней)
- Обвязка под перегородку (только низ, без стоек)
- Окно / витраж: перемычка сверху, ригель снизу
- Дверь: в наружной стене — перемычка; во внутренней — без каркаса

Решения по каркасу


1. Всё из трубы 80×80 (стенка 3 мм), сварка.
2. Домик на сваях: нижняя обвязка — несущая рама пола, сплошная по всему контуру и под перегородками, в дверях не разрезается.
3. Наружные стены — труба внутрь от наружной грани; оси перегородок — по исходному плану.
4. Стойки — только в наружных стенах: в углах, по обе стороны проёмов и промежуточные с шагом не более 2000 мм (размеры — по осям).
5. Над проёмами наружных стен — перемычка, под окнами (низ 900) — подоконный ригель.
6. Перегородки — без металлических стоек и верхней обвязки: ставятся лёгкими (дерево / ГКЛ) на обвязку под перегородку.
7. Пролёты обвязок 9400 и 7540 — из хлыста 12 м; сваи — под углами, примыканиями перегородок и по нижней обвязке с шагом по расчёту.
8. Крыша, раскосы, балки пола и оголовки свай — по отдельному расчёту.

Стоек: 25 шт. · Трубы всего: 167.6 м


Спецификация и раскрой — лист 2

Металлический каркас домика — 3D и спецификация

Труба профильная 80×80×3 | Обвязки — серые, под перегородками — коричневые, стойки — синие, перемычки — оранжевые, ригели — зелёные

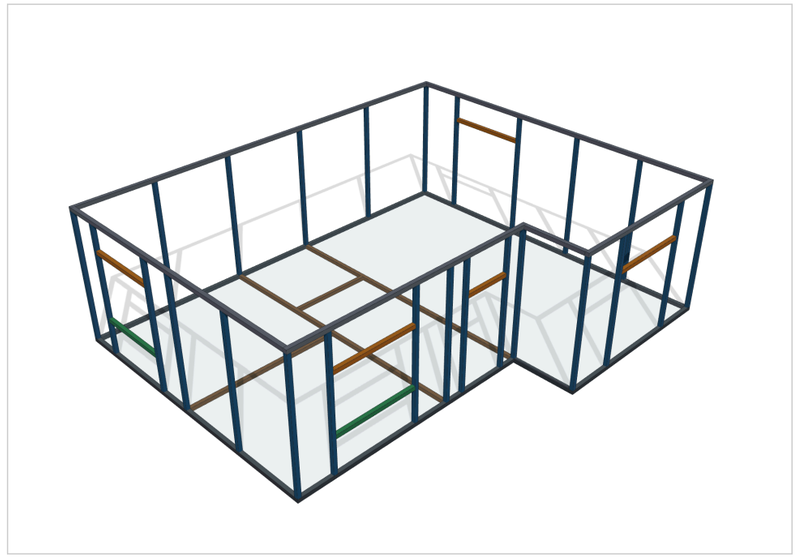


Вид с юго-запада (стены 1, 2, 3, 6)

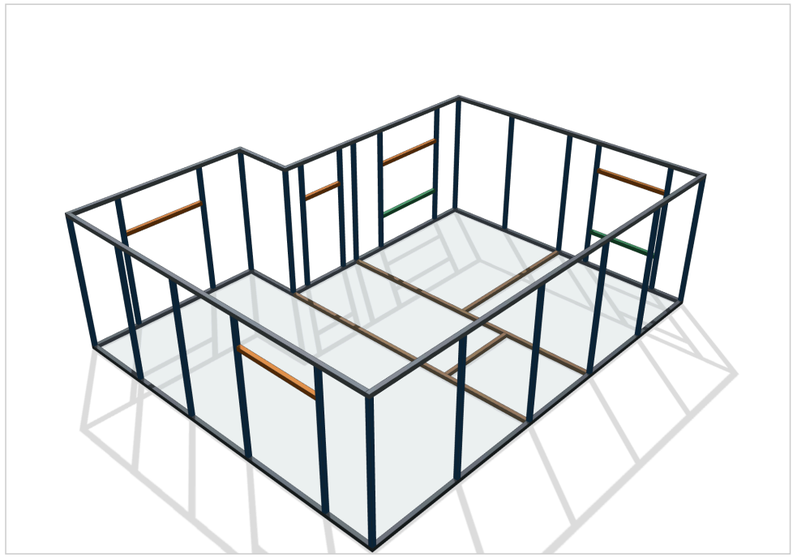

Вид с северо-востока (стены 4, 5); пол показан прозрачным

Раскрой на хлысты 12 м (пропил 3 мм)

Хлыстов: 15 шт. = 180 м, отход 12.4 м (7%)

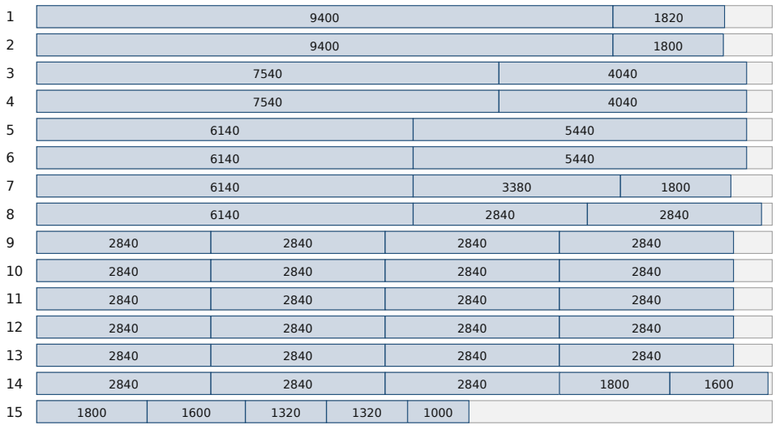

Примечания

• Масса: 7.07 кг/м для 80×80×3 (ГОСТ 30245); при стенке 4 мм — ≈ 9,2 кг/м, масса вырастет примерно на 30%.

• Длинные обвязки 9400 и 7540 — цельными из хлыста 12 м; если хлысты 6 м — стык со вставкой-накладкой над стойкой.

• Запас на брак и подгонку — +5% к закупке.

• Раскосы жёсткости в углах и кровля в расчёт не входят.

Спецификация (длины по факту реза)

№	Элемент	Длина, мм	Кол-во	Всего, м	Масса, кг
1	нижняя обвязка	9400	1	9.40	66.5
2	нижняя обвязка	7540	1	7.54	53.3
3	нижняя обвязка	6140	1	6.14	43.4
4	нижняя обвязка	5440	1	5.44	38.5
5	нижняя обвязка	4040	1	4.04	28.6
6	нижняя обвязка	1320	1	1.32	9.3
7	обвязка под перегородку	6140	2	12.28	86.8
8	обвязка под перегородку	3380	1	3.38	23.9
9	обвязка под перегородку	1820	1	1.82	12.9
10	верхняя обвязка	9400	1	9.40	66.5
11	верхняя обвязка	7540	1	7.54	53.3
12	верхняя обвязка	6140	1	6.14	43.4
13	верхняя обвязка	5440	1	5.44	38.5
14	верхняя обвязка	4040	1	4.04	28.6
15	верхняя обвязка	1320	1	1.32	9.3
16	стойка	2840	25	71.00	502.0
17	перемычка	1800	3	5.40	38.2
18	перемычка	1600	1	1.60	11.3
19	перемычка	1000	1	1.00	7.1
20	подоконный ригель	1800	1	1.80	12.7
21	подоконный ригель	1600	1	1.60	11.3
	ИТОГО		**48**	**167.6**	**≈ 1185**