


ВИД А — ОСНОВНАЯ СТЕНА (фасад)

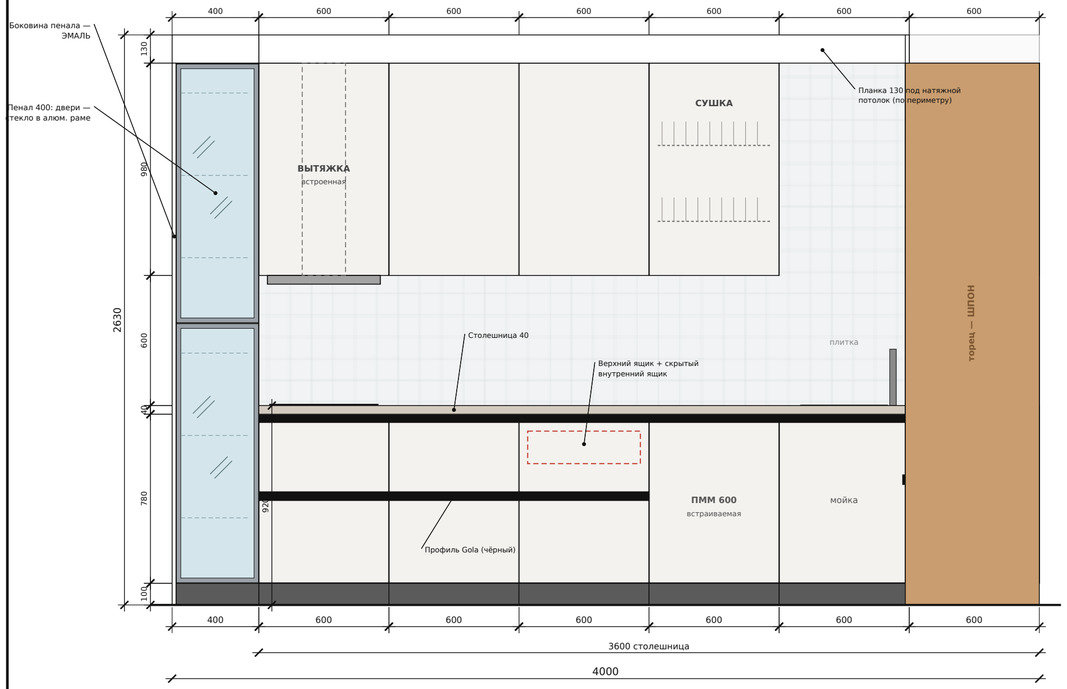


ВИД Б — ПРАВАЯ СТЕНА

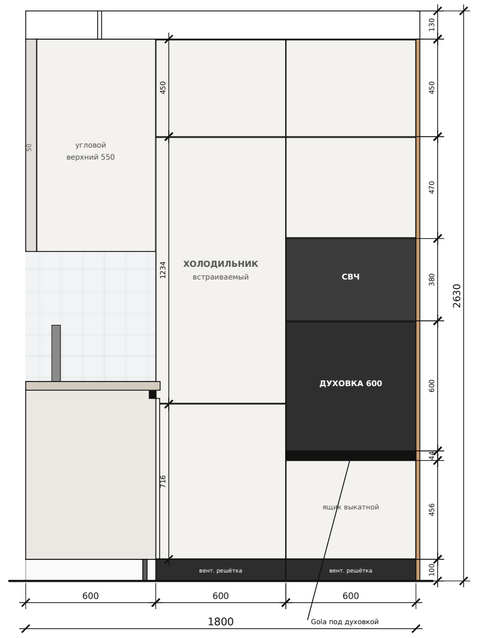

ВИД С УГЛА

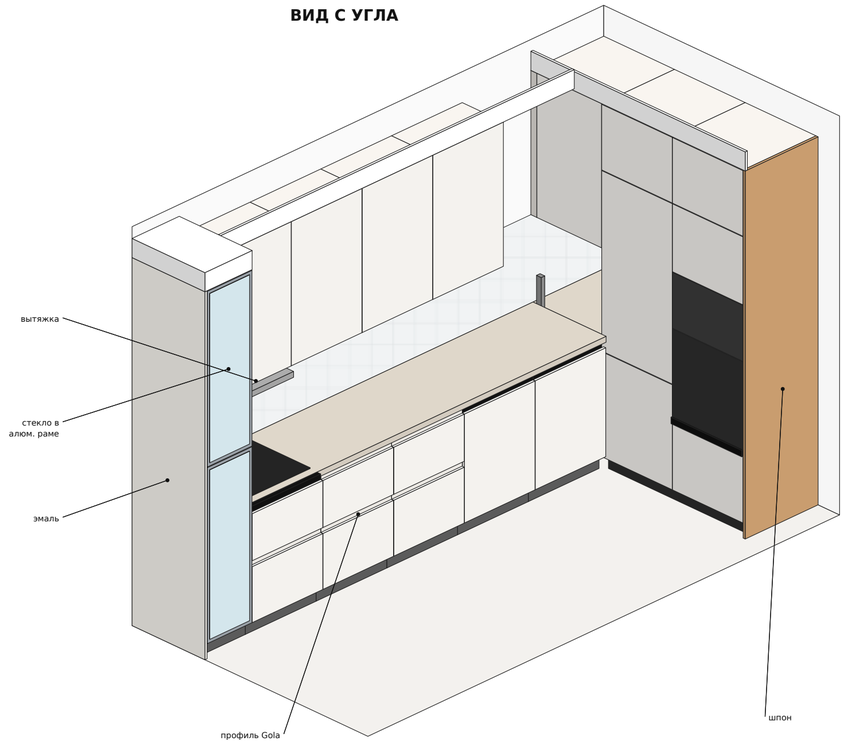

ПЛАН

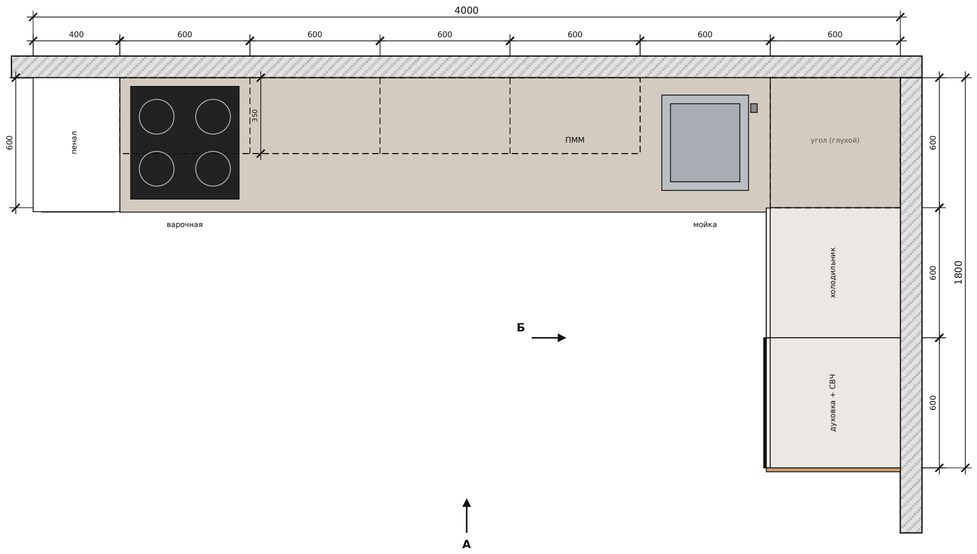

СОСТАВ И МАТЕРИАЛЫ

Пенал 400 (слева): 2 двери — стекло в алюминиевой раме, полки внутри; левая боковина — ЭМАЛЬ

Нижний ряд без ручек: профиль Gola чёрный (верхний под столешницей и средний между ящиками)

Модули 600: под варочной — 2 ящика; 2-й — 2 ящика; 3-й — 2 ящика, в верхнем скрытый внутренний ящик

4-й — ПММ 600 встраиваемая (один фасад); 5-й — под мойку (один фасад); угол 600 — глухой

Высота низа 920 = цоколь 100 + корпус 780 + столешница 40; столешница 3600 до правой стены

Фартук 600 — плитка (после кухни); над мойкой верхнего шкафа нет

Верхний ряд 980 (низ 1520, верх 2500): шкаф со встроенной вытяжкой над варкой, сушка у мойки

Правая стена: угловой верхний 550 + планка 50; колонна холодильника (фасады 716 / 1234 / 450)

Колонна духовки: ящик выкатной под духовкой + Gola, духовка 600, СВЧ 380, фасады 466 и 450

Правый торец колонн — ШПОН; вентиляционные решётки в цоколе колонн

Планка 130 под натяжной потолок по всему периметру; общая высота кухни 2630

МАТЕРИАЛЫ ФАСАДОВ

- Фасады — по выбору заказчика (на чертеже светлые)
- Эмаль — левая боковина пенала
- Шпон — правый торец колонн
- Стекло в алюминиевой раме — двери пенала
- Профиль Gola — чёрный

КУХНЯ УГЛОВАЯ

Общий вид: фасады, план, вид с угла (по эскизу от 06.10.26)

Основная стена 4000 (столешница 3600), правая 1800 Высота 2500 + планка 130 = 2630 мм	Масштаб **1:20**
Все размеры в миллиметрах Цоколь 100, столешница 40, низ 920	Лист **1 (A2)**