


РАЗВЁРТКИ СТЕН. ГАРДЕРОБНАЯ

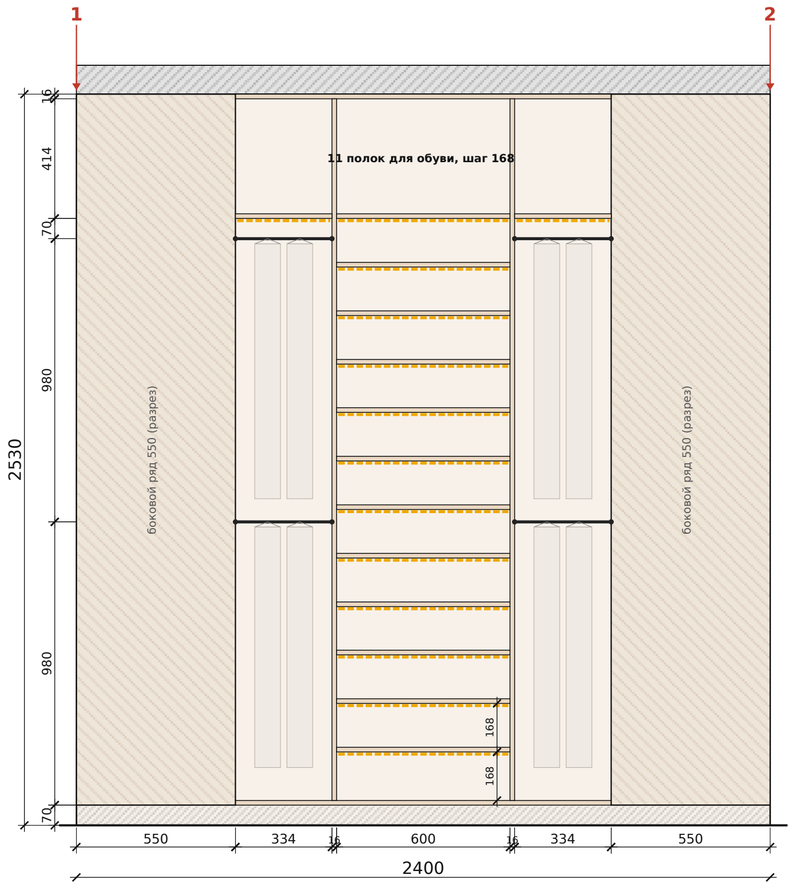

РАЗВЁРТКА 1–2 (задняя стена)

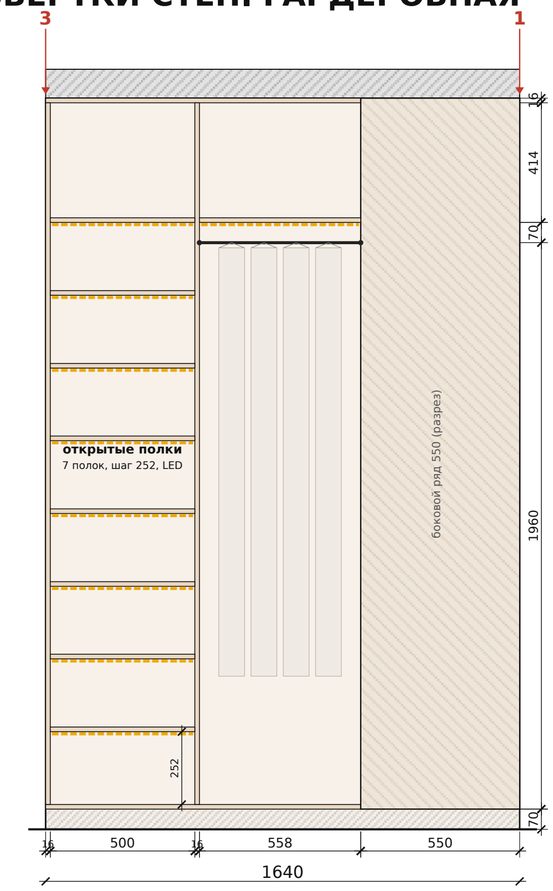


РАЗВЁРТКА 3–1 (левая стена)

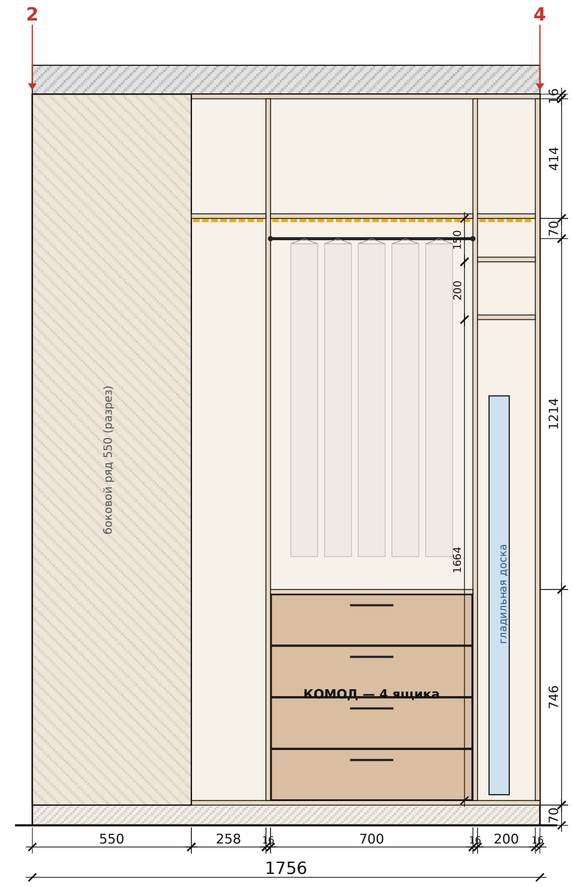

РАЗВЁРТКА 2–4 (правая стена)

ПЛАН

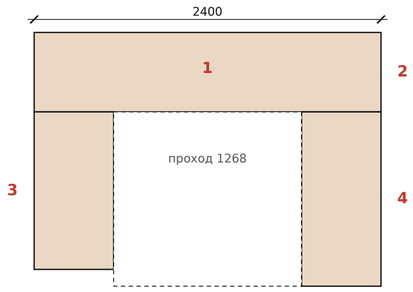

УСЛОВНЫЕ ОБОЗНАЧЕНИЯ

- LED-лента в профиле по переднему краю полок
- штанга
- боковой ряд в разрезе
- цоколь 70

ПРИМЕЧАНИЕ

1. Корпус ЛДСП 16, глубина 550, высота 2530, цоколь 70.
2. Размеры ниш по полу — в свету (по 3D-модели): 334 / 600 / 334; 558 / 500; 258 / 700 / 200.
3. Высоты полок и штанг — уточнить по месту; штанги 2 яруса: 2030 и 1050.
4. Подсветка — в каждой открытой полке и под полкой антресоли.

ГАРДЕРОБНАЯ П-ОБРАЗНАЯ

развёртки стен

Высота 2530, глубина 550, цоколь 70

Корпус ЛДСП 16

Размеры в мм

Масштаб 1:15

Лист 1