
ПЛАН РАССАДКИ ДЕКОРАТИВНОЙ ЗОНЫ

от террасы до газовой трубы · костровая зона справа · вид сверху, дом слева

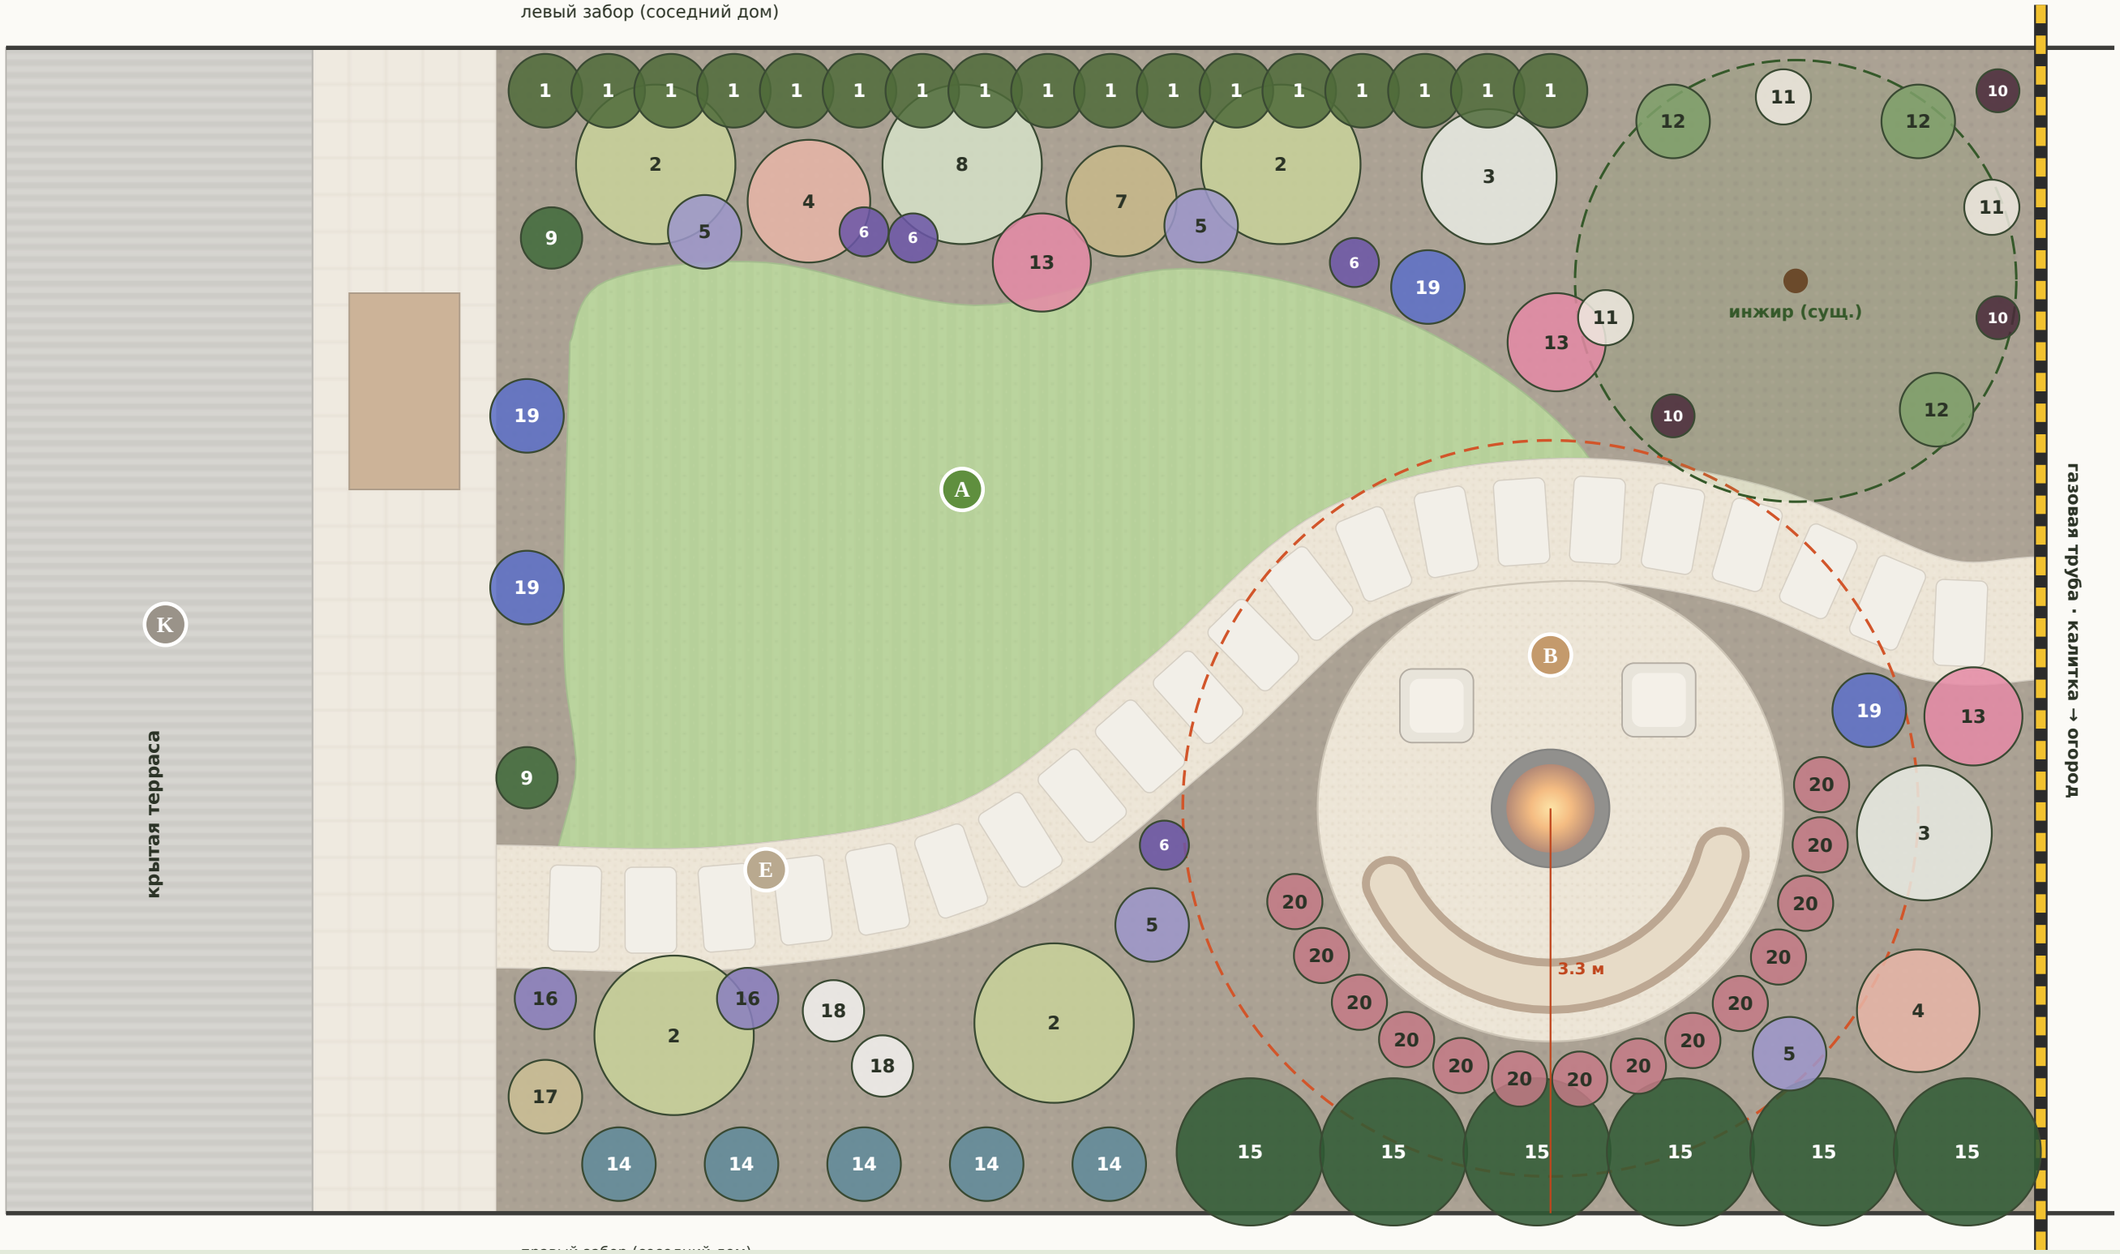

ПРИНЦИПЫ

Слева — многоярусный миксбордер: изгородь, кустарники, многолетники; в конце — тенистый уголок под инжиром.

Справа у террасы — колоновидные можжевельники, дальше вдоль костра — лавровишня (широколистная, сочная, слабо горит).

Костёр обрамлён кольцом очитка (суккулент) — живая противопожарная кайма.

Злаки, хвойные, лаванда и розы — не ближе 3 м от чаши.

Между плит у террасы — тимьян ползучий, ~1 м² (8–10 шт.).

Тюльпаны 40–60 шт. группами между многолетниками слева.

Мульча — кора сосны; у костра — гравий.

— — — R 3 м от чаши: без хвойных, злаков и сухостоя

Масштаб 1:50 (А3)

0 1 2 3 4 5 м

АССОРТИМЕНТ И КОЛИЧЕСТВО

Климат Краснодарского края · размеры — диаметр куста во взрослом виде

1	**Кизильник блестящий *живая изгородь*** вдоль левого забора, 2 шт/пог, м · Ø 0,6 м	17 шт.	8	**Дерен белый *'Elegantissima'*** красные побеги зимой · Ø 1,3 м	1 шт.	15	**Лавровишня *'Novita'*** вечнозелёный экран у костра (слабо горюча) · Ø 1,2 м	6 шт.
2	**Гортензия метельчатая *'Limelight'*** солнце / полутень · Ø 1,3 м	4 шт.	9	**Самшит (стриженый шар) *Ø 40–50 см*** акценты у входа на дорожку · Ø 0,5 м	2 шт.	16	**Лаванда узколистная *'Hidcote'*** вдоль дорожки у террасы · Ø 0,5 м	2 шт.
3	**Спирея серая *'Grefsheim'*** цветёт в апреле · Ø 1,1 м	2 шт.	10	**Гейхера *'Obsidian'*** под инжиром · Ø 0,3 м	3 шт.	17	**Пеннисетум *'Hameln'*** у террасы, далеко от огня · Ø 0,6 м	1 шт.
4	**Роза парковая *'The Generous Gardener'*** дальше 3 м от чаши · Ø 1,0 м	2 шт.	11	**Астильба *'Deutschland'*** под инжиром, полив · Ø 0,5 м	3 шт.	18	**Флокс метельчатый *'David'*** белый, июль–сентябрь · Ø 0,5 м	2 шт.
5	**Котовник Фассена *'Walker's Low'*** куртины у дорожки · Ø 0,6 м	4 шт.	12	**Хоста *крупнолистная*** тень от инжира · Ø 0,6 м	3 шт.	19	**Герань крупнокорневищная *'Rozanne'*** почвопокровник, кайма · Ø 0,6 м	4 шт.
6	**Шалфей дубравный *'Caradonna'*** передний план · Ø 0,4 м	4 шт.	13	**Пион травянистый *розовый, махровый*** весеннее цветение · Ø 0,8 м	3 шт.	20	**Очиток видный *'Herbstfreude'*** кольцо у костровой площадки (не горит) · Ø 0,5 м	14 шт.
7	**Мискантус китайский *'Gracillimus'*** только у левого забора, далеко от огня · Ø 0,9 м	1 шт.	14	**Можжевельник скальный *'Blue Arrow'*** экран у террасы, ≥ 4,5 м от чаши · Ø 0,6 м	5 шт.			

Всего растений: 83 шт. (без луковичных и тимьяна) · лист 2