

ЛЕВАЯ СТЕНА

развёртка, вид изнутри

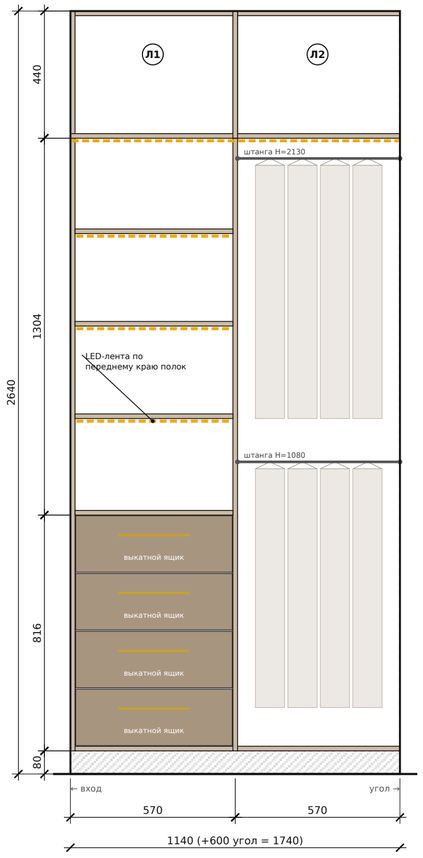


ЗАДНЯЯ СТЕНА (напротив входа)

фасад, вид от входа

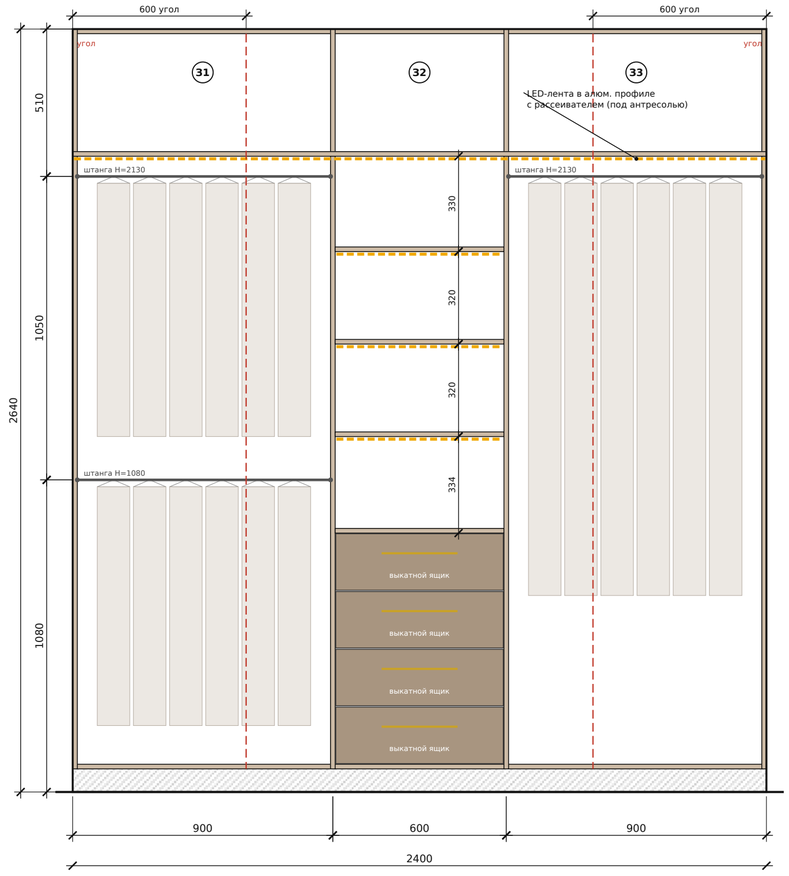


ПРАВАЯ СТЕНА

развёртка, вид изнутри

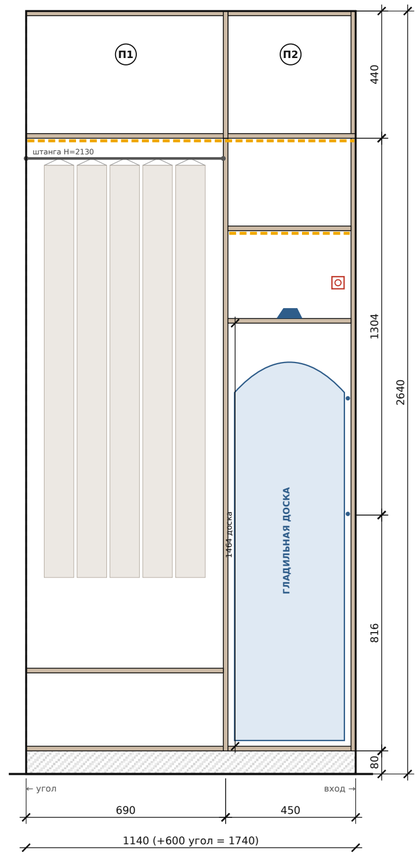

ПЛАН (вид сверху)

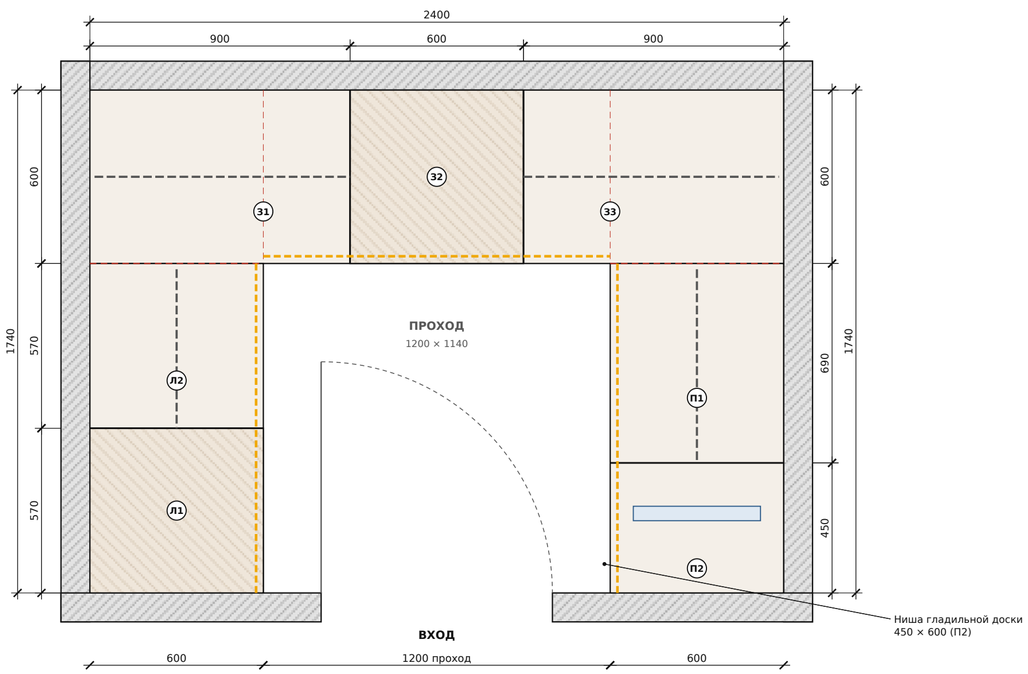

ИСХОДНЫЕ ДАННЫЕ

Комната: ширина 2400 × глубина 1740 (стены слева/справа) × высота 2640
Планировка П-образная, глубина гардеробной (корпусов) — 600 мм
Проход между боковыми секциями — 1200 мм
Материал: ЛДСП 16 мм (цвет «серо-коричневый»), кромка ПВХ 2 мм
Цоколь 80 мм, ящики — фасады 200 мм, ручки-скобы латунь
Антресоль с низа 2200 до потолка 2640, верхняя штанга H=2130
LED: лента 24 В, 4000 K, блок питания в антресоли, датчик открытия двери
Гладильная доска справа у входа (П2); при необходимости
ниша П2 переносится зеркально на левую сторону
Размеры уточнить по месту после замера и чистовой отделки стен

УСЛОВНЫЕ ОБОЗНАЧЕНИЯ

- LED-лента 24 В в алюм. профиле с рассеивателем
- Выкатной ящик (направляющие полного выдвижения, доводчик)
- Штанга для плечиков (овальная, хром/золото)
- Гладильная доска (вертикальное хранение)
- Граница угловой зоны / открыто в угол
- Розетка 220 В (для утюга/отпаривателя)

СЕКЦИИ

Л1	570	4 выкатных ящика + 3 полки с LED (сложенные вещи)
Л2	570	2 яруса штанг (короткая одежда), открыта в угол
З1	900	2 яруса штанг (рубашки, юбки, брюки), угловая зона
З2	600	4 выкатных ящика + 3 полки с LED (сумки)
З3	900	Длинная одежда (пальто, платья), угловая зона
П1	690	Длинная одежда + полка для обуви H=350, открыта в угол
П2	450	Ниша гладильной доски: доска, полка утюга (H=1560), розетка
—	2400	Антресоль H=424 по всему периметру, LED снизу

ГАРДЕРОБНАЯ КОМНАТА

Чертёж общего вида: план, развёртка стен

Габариты: 2400 × 1740 × 2640 мм Глубина корпусов: 600 мм	Масштаб **1:15**
Все размеры в миллиметрах ЛДСП 16 мм	Лист **1 (A2)**