
ЛИСТ 1 — ПАНЕЛЬ КОРОБА ИНСТАЛЛЯЦИИ

ЛДСП 2800 × 2070, деталь 2050 × 1154

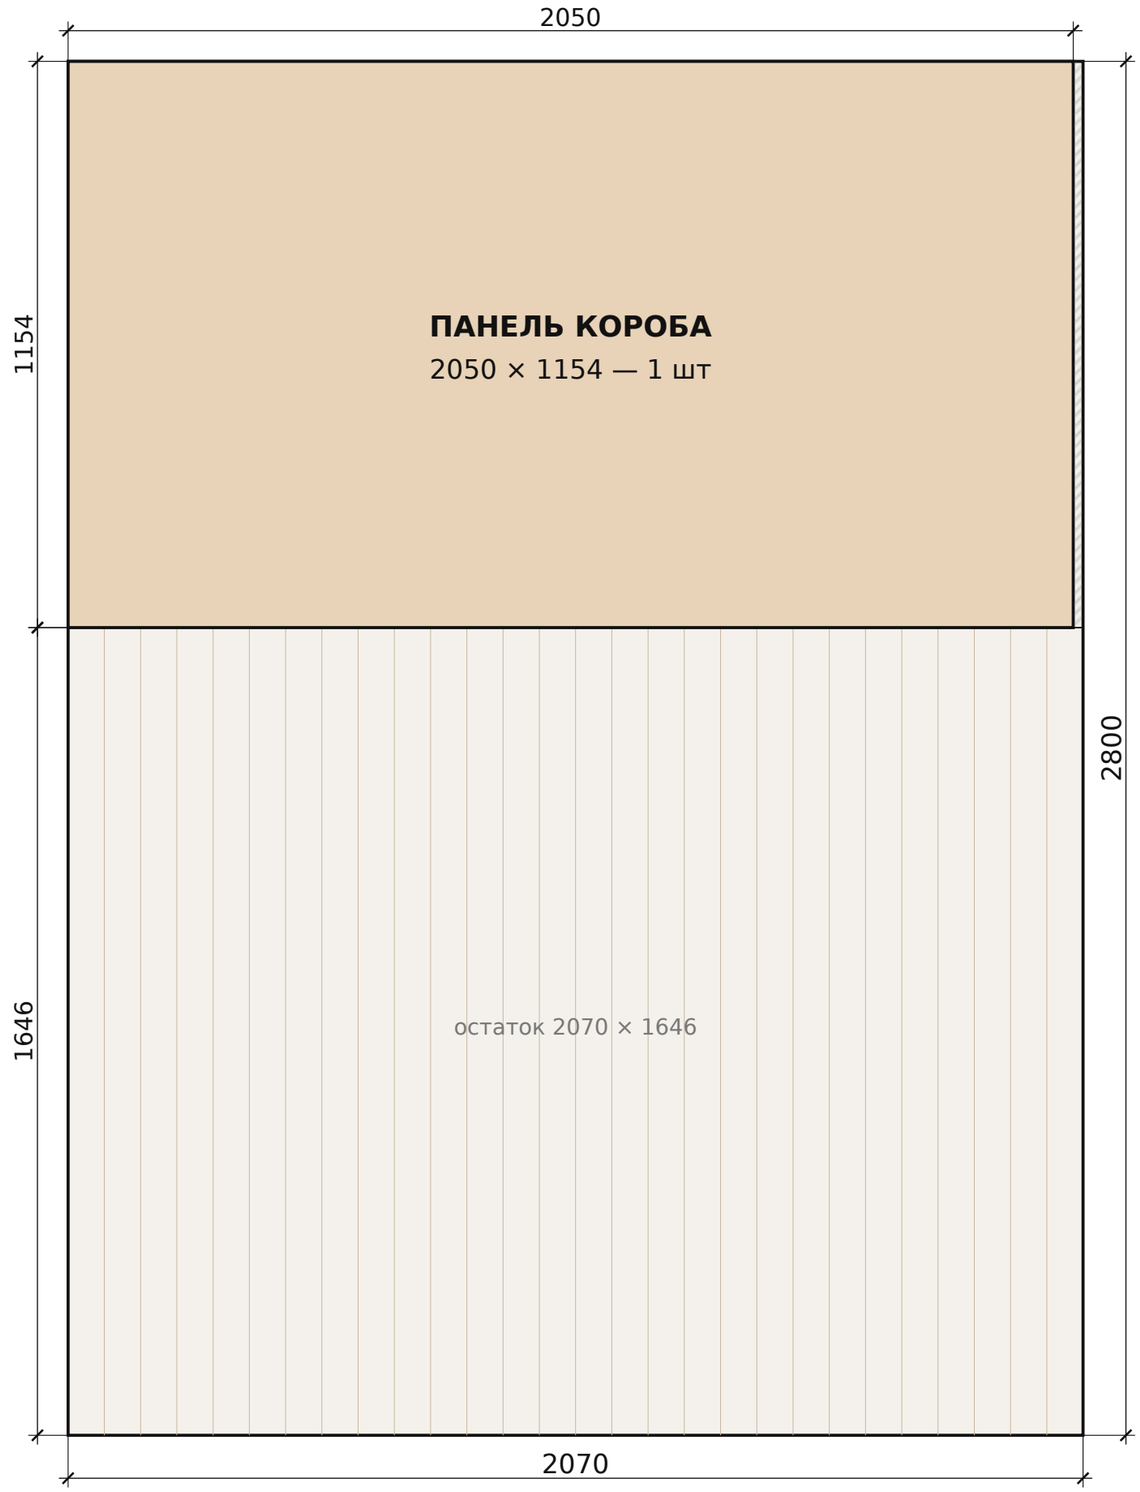

деталь


деловой остаток

отход / промежуток

Лист ЛДСП 2800 × 2070 · размеры в мм

ЛИСТ 2 — ФАСАДЫ ШКАФОВ 860

ЛДСП 2800 × 2070, 4 фасада 415 × 1782 с промежутками 30 и 330

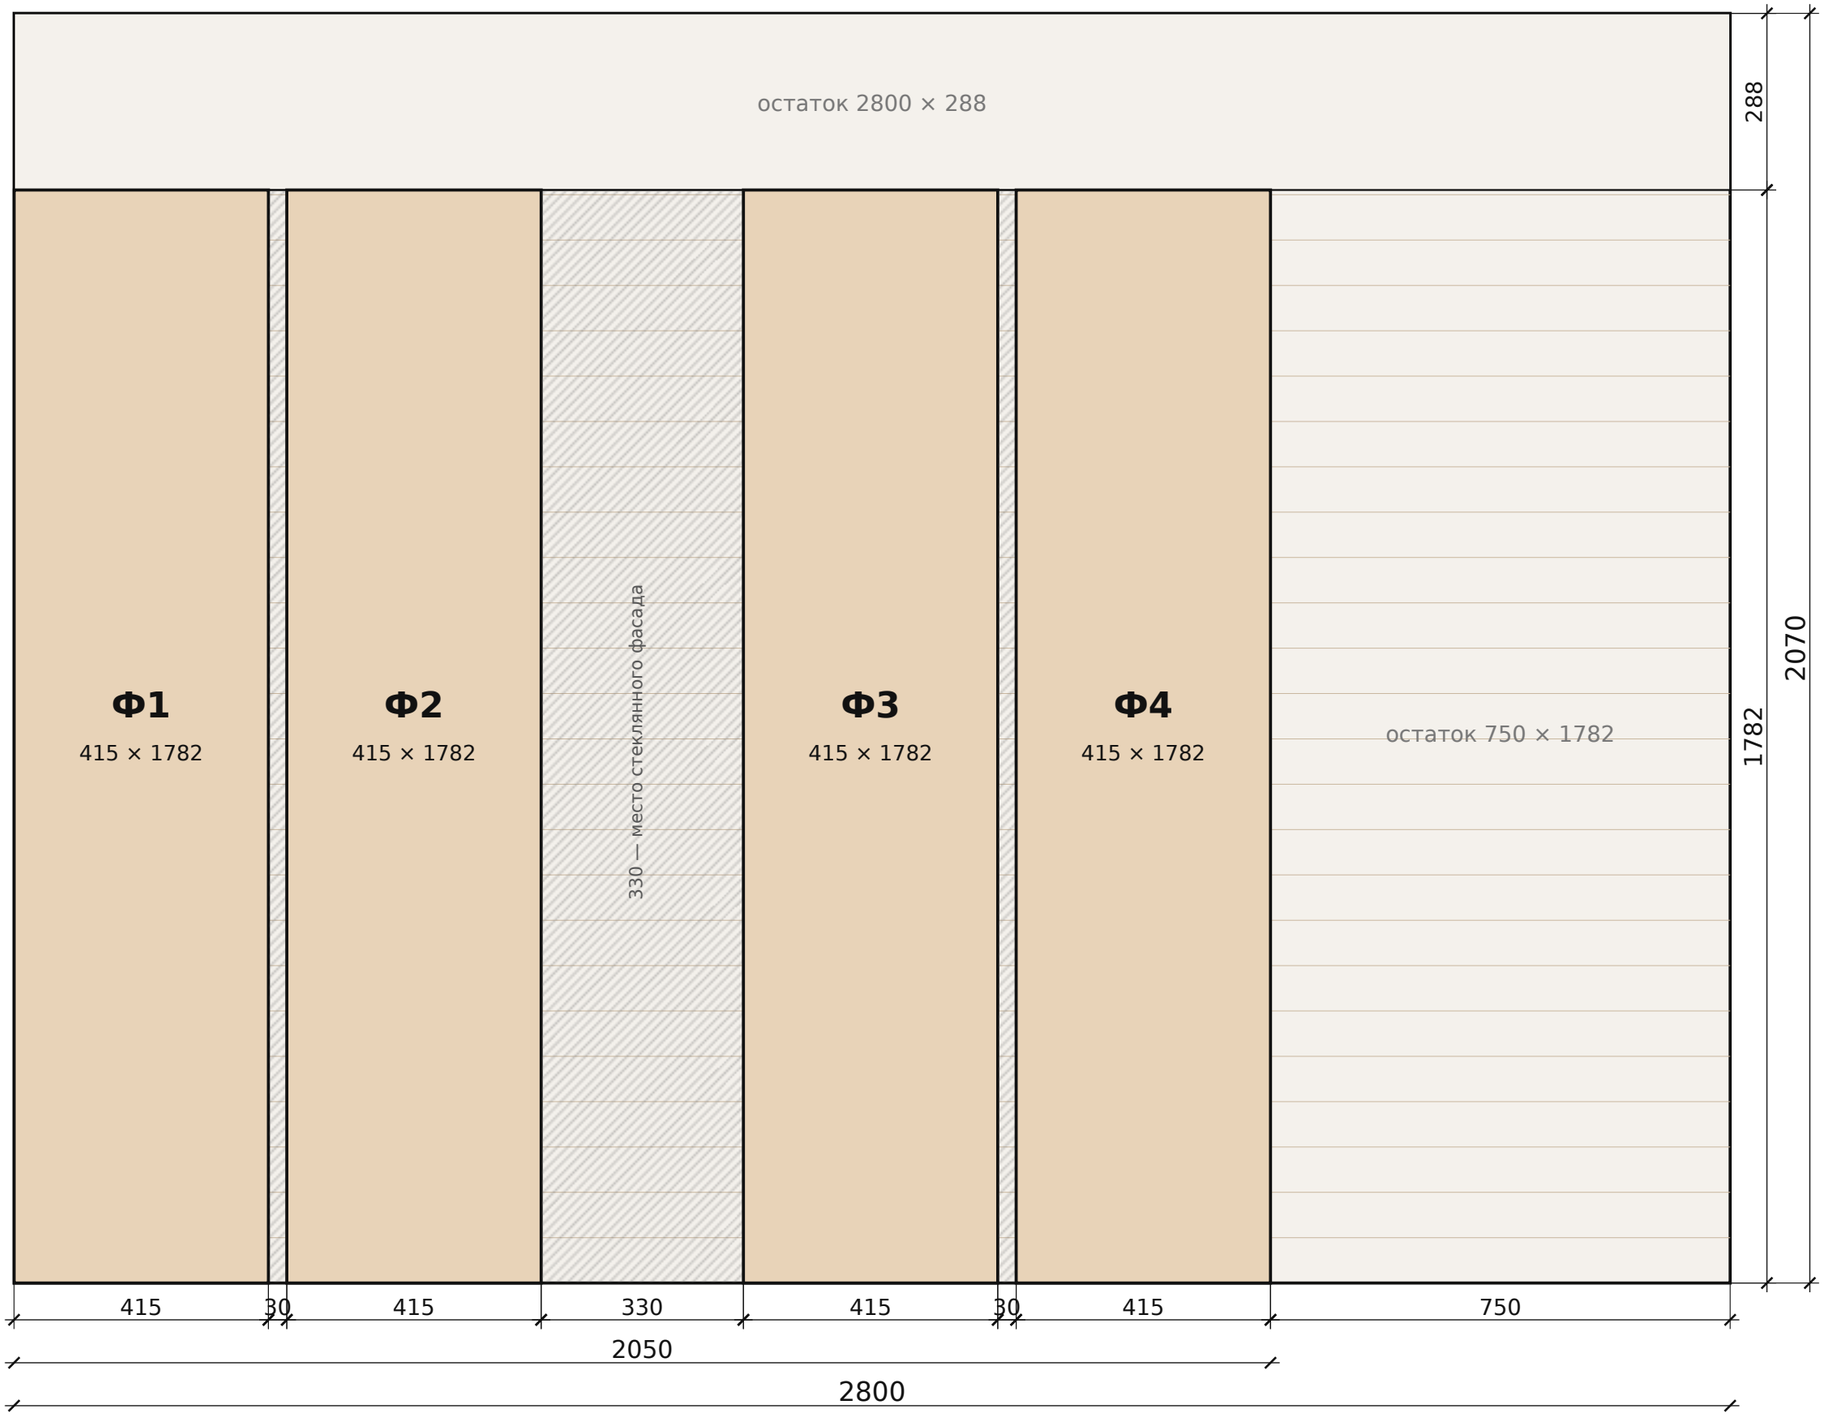

деталь

деловой остаток

отход / промежуток

Фасады выкроены подряд — рисунок декора непрерывный