

ВИД А — ОСНОВНАЯ СТЕНА (фасад)

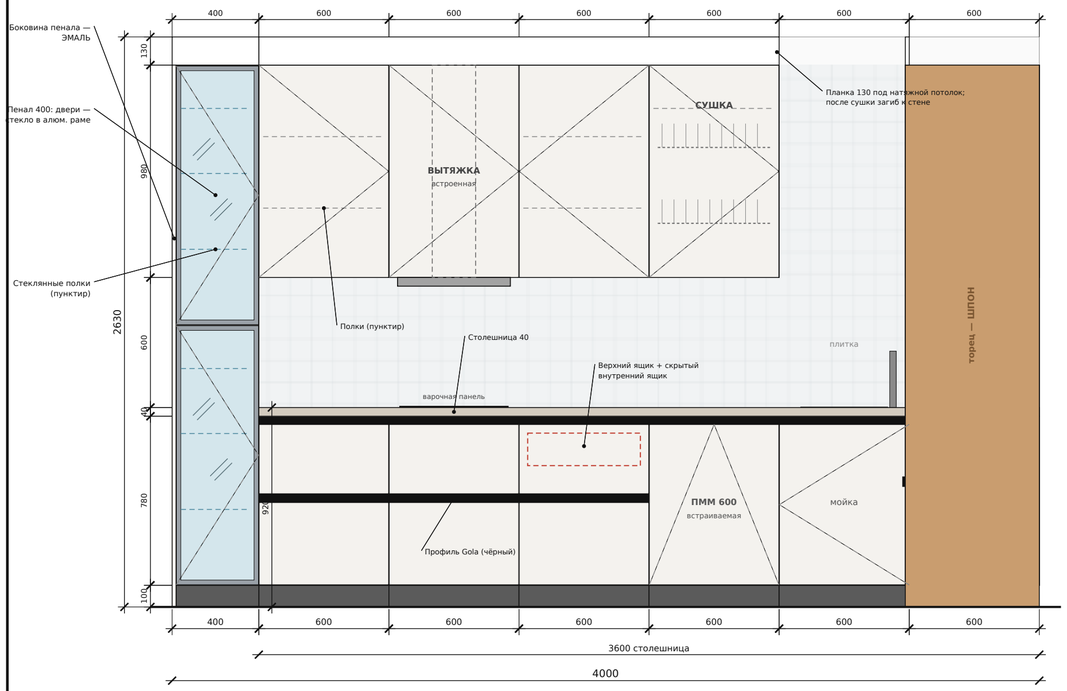


ВИД Б — ПРАВАЯ СТЕНА


все фасады правой стены — ШПОН

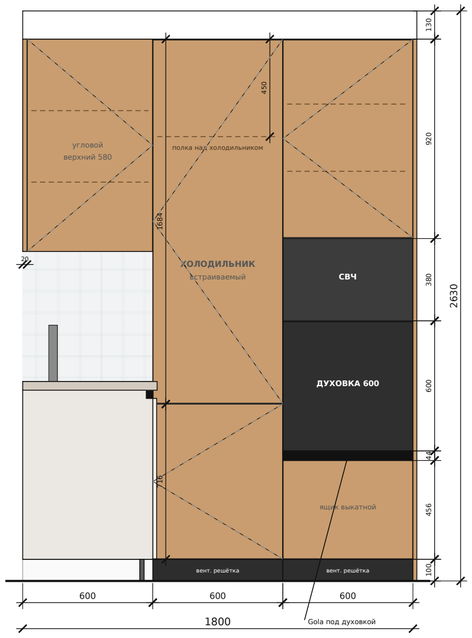

ВИД С УГЛА

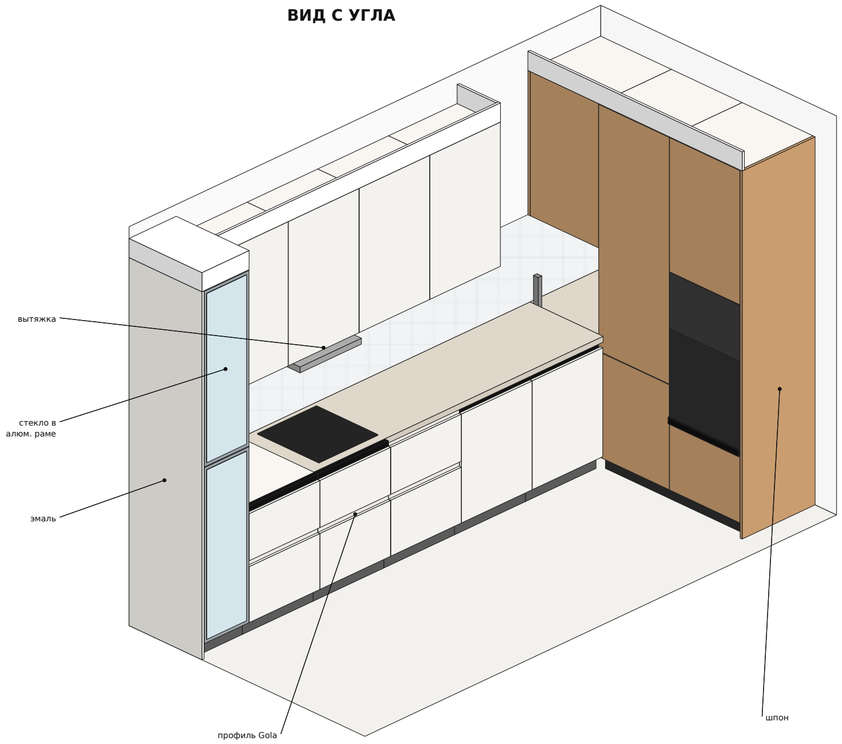

ПЛАН

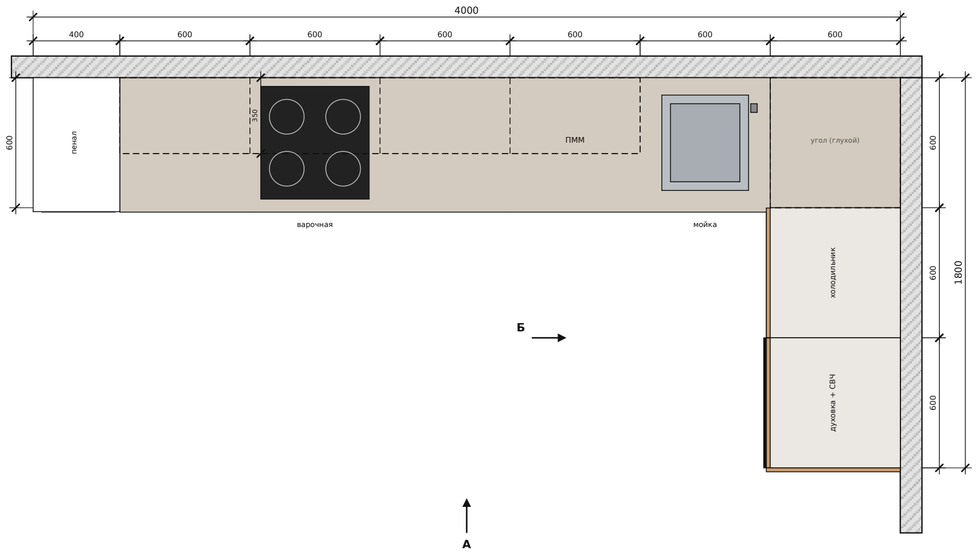

СОСТАВ И МАТЕРИАЛЫ

Пенал 400 (слева) — витрина: 2 двери, стекло в алюм. раме, СТЕКЛЯННЫЕ полки; левая боковина — ЭМАЛЬ

Нижний ряд без ручек: профиль Gola чёрный (верхний под столешницей и средний между ящиками)

Модули 600: 1-й — 2 ящика; 2-й — под варочной, 2 ящика; 3-й — 2 ящика, в верхнем скрытый внутр. ящик

4-й — ПММ 600 встраиваемая (один фасад); 5-й — под мойку (один фасад); угол 600 — глухой

Высота низа 920 = цоколь 100 + корпус 780 + столешница 40; столешница 3600 до правой стены

Фартук 600 — плитка (после кухни); над мойкой верхнего шкафа нет

Верхний ряд 980: 1-й и 3-й — по 2 полки; 2-й — встроенная вытяжка над варкой; 4-й — сушка + полка

Правая стена — ФАСАДЫ ШПОН: угловой верхний 580 + планка 20 (2 полки); холодильник: 716 + 1684, над ним полка (отсек 450)

Колонна духовки: ящик выкатной + Gola, духовка 600, СВЧ 380, над СВЧ один фасад 920 (2 полки)

Планка 130 под натяжной потолок по периметру; над верхними — до сушки и загиб к стене; общая высота 2630

Все полки на чертеже — лёгкий пунктир; стеклянные полки витрины — голубой пунктир

МАТЕРИАЛЫ ФАСАДОВ

- Фасады — по выбору заказчика (на чертеже светлые)
- Эмаль — левая боковина пенала
- Шпон — все фасады правой стены и правый торец
- Стекло в алюминиевой раме — двери пенала
- Профиль Gola — чёрный
- Открывание: вершина треугольника — сторона ручки, основание — петли

КУХНЯ УГЛОВАЯ

Общий вид: фасады, план, вид с угла (по эскизу от 06.10.26)

Основная стена 4000 (столешница 3600), правая 1800 Высота 2500 + планка 130 = 2630 мм	Масштаб **1:20**
Все размеры в миллиметрах Цоколь 100, столешница 40, низ 920	Лист **1 (A2)**