

ФАСАД — ОСНОВНАЯ СТЕНА

по заводскому чертежу «Габариты изделия»

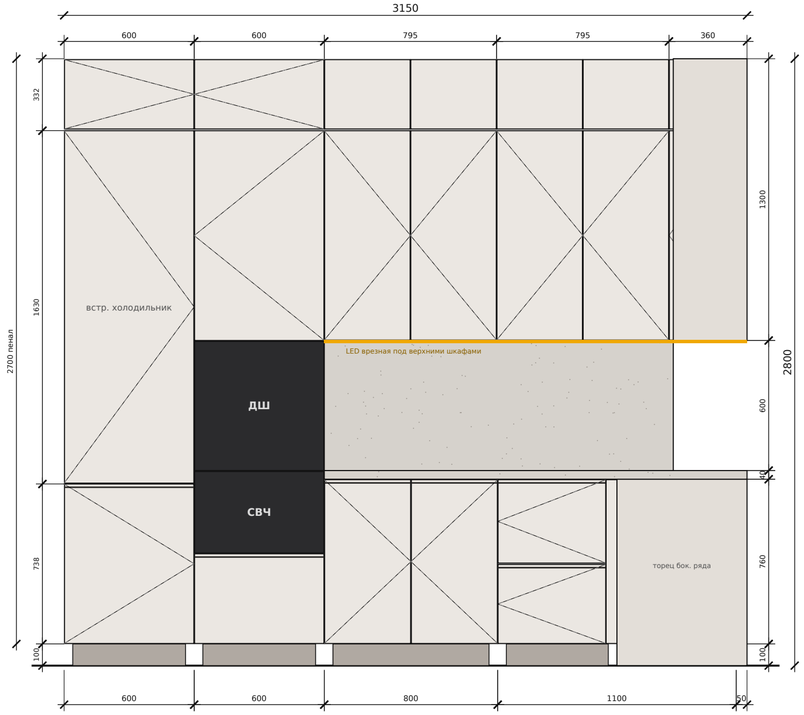


ФАСАД — БОКОВАЯ СТЕНА

мойка, ПММ 450, сушилка

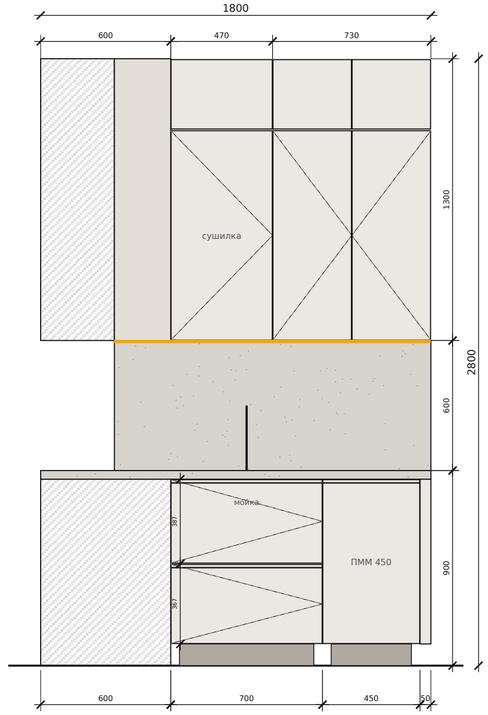


ОСТРОВ

из дизайн-проекта, ящики к кухне

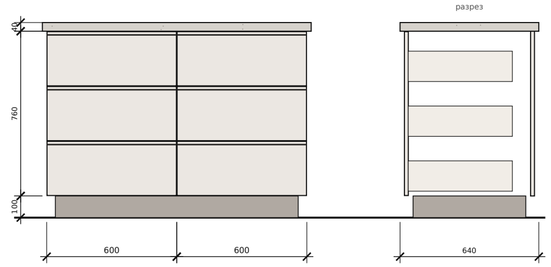

ПЛАН

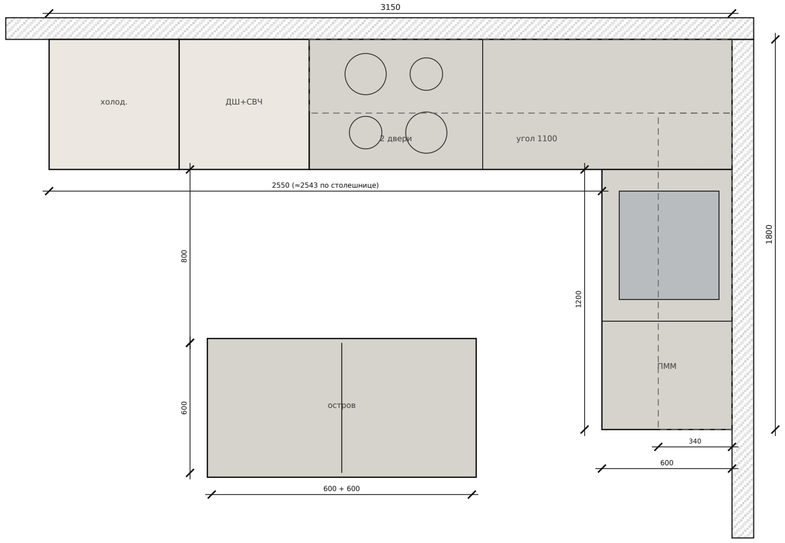

ПРИМЕЧАНИЯ

Габариты — по заводскому чертежу: основная стена 3150, боковая 1800, высота 2800.

Опоры 100, нижние корпуса до 860, столешница 40, фартук 600, верхние шкафы 1300 (два ряда фасадов, верх 318).

Пенал холодильника 600: нижняя дверца, встроенный холодильник, верхняя дверца.

Пенал 600: ящик, СВЧ, духовой шкаф, дверца (полки 300), верхняя дверца.

Основной ряд: модуль 800 (2 двери), угловой 1100 (фасад 500 в два яруса 365 / 363 + планка 50).

Боковой ряд: мойка 700 (две дверцы ярусами), ПММ 450, планка 50; над мойкой — сушилка (470).

Верхние шкафы: 795 / 795 / 360 и 470 / 730, глубина 340.

Материалы корпуса и фасадов — ЛДСП Egger; фурнитура Blum; подсветка врезная.

Открывание: низ — интегрированная ручка, верх — Push.

Остров 1200 × 600 — из дизайн-проекта (в заводском чертеже нет). * Варочная — уточнить место.

КУХОННЫЙ ГАРНИТУР

угловой + остров

3150 × 1800 × 2800 мм

ЛДСП Egger, Blum

Размеры в мм

Масштаб **1:20**

Лист 1 (A2)