


РАЗВЁРТКИ СТЕН. ГАРДЕРОБНАЯ

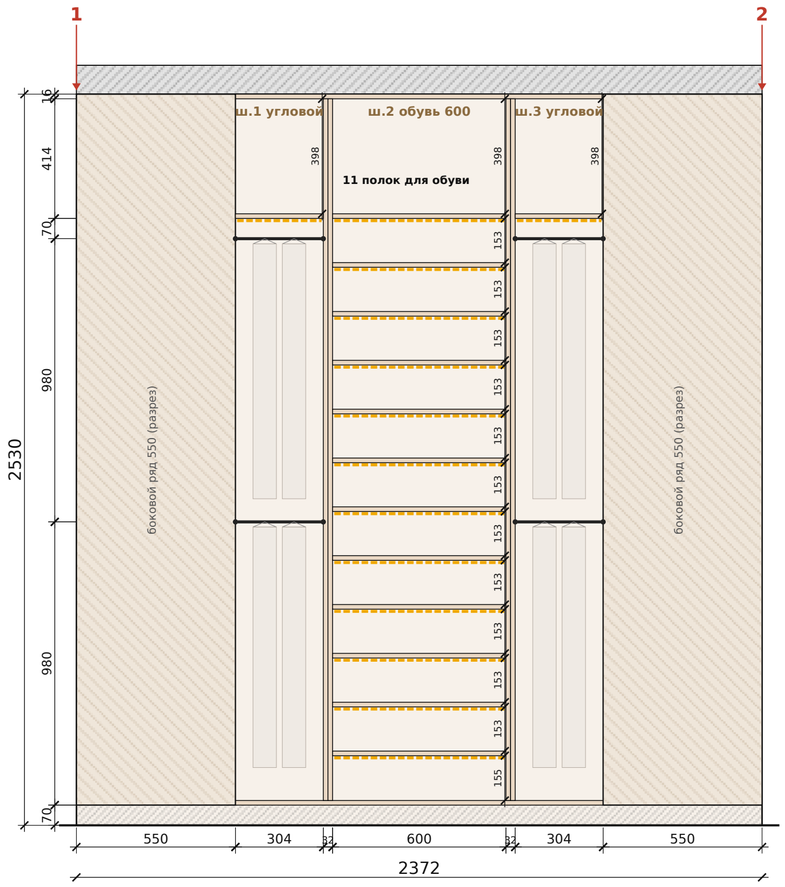

РАЗВЁРТКА 1–2 (задняя стена)

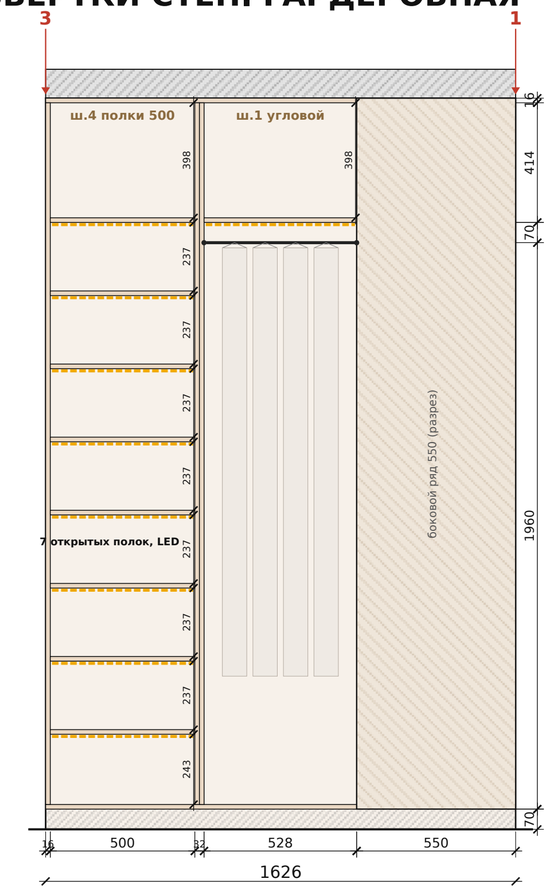


РАЗВЁРТКА 3–1 (левая стена)

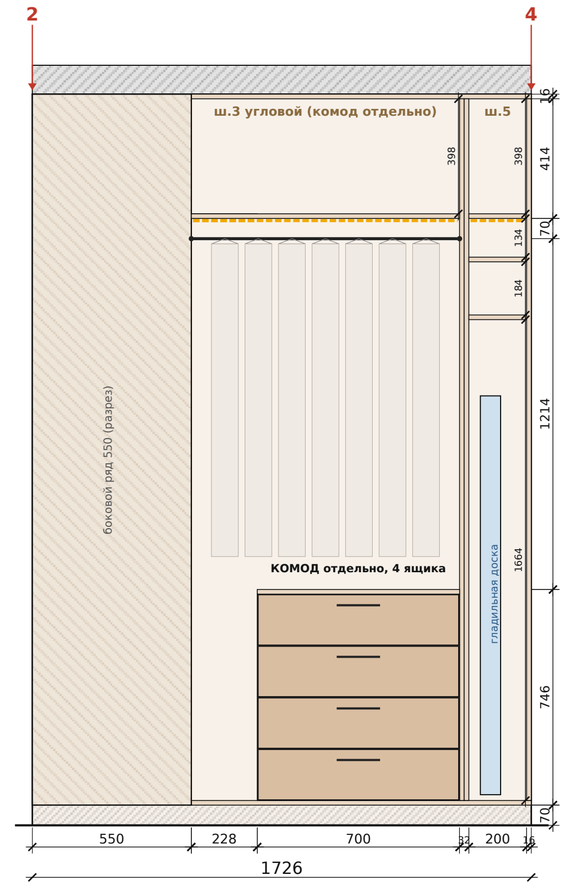

РАЗВЁРТКА 2–4 (правая стена)

ПЛАН

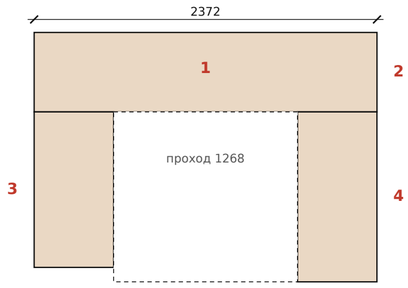

УСЛОВНЫЕ ОБОЗНАЧЕНИЯ

- LED-лента в профиле по переднему краю полок
- штанга
- боковой ряд в разрезе
- цоколь 70

ПРИМЕЧАНИЕ

1. Корпус ЛДСП 16, глубина 550, высота 2530, цоколь 70.
2. 5 отдельных шкафов: 2 угловых, 500 (полки), 600 (обувь), 200 (гладильная доска); на стыках 16 + 16.
Размеры ниш — в свету: 304 / 600 / 304; 528 / 500; 228 + 700 / 200. Комод 700 — отдельно стоящий.
Задняя стенка ЛДСП 16 по периметру: корпус 534 + 16 = 550; глубина полок 530.
3. Высоты полок и штанг — уточнить по месту; штанги 2 яруса: 2030 и 1050.
4. Подсветка — в каждой открытой полке и под полкой антресоли.

ГАРДЕРОБНАЯ П-ОБРАЗНАЯ

развёртки стен

Высота 2530, глубина 550, цоколь 70

Корпус ЛДСП 16

Размеры в мм

Масштаб 1:15

Лист 1