

ФАСАД — СТЕНА 2–7

двери закрыты

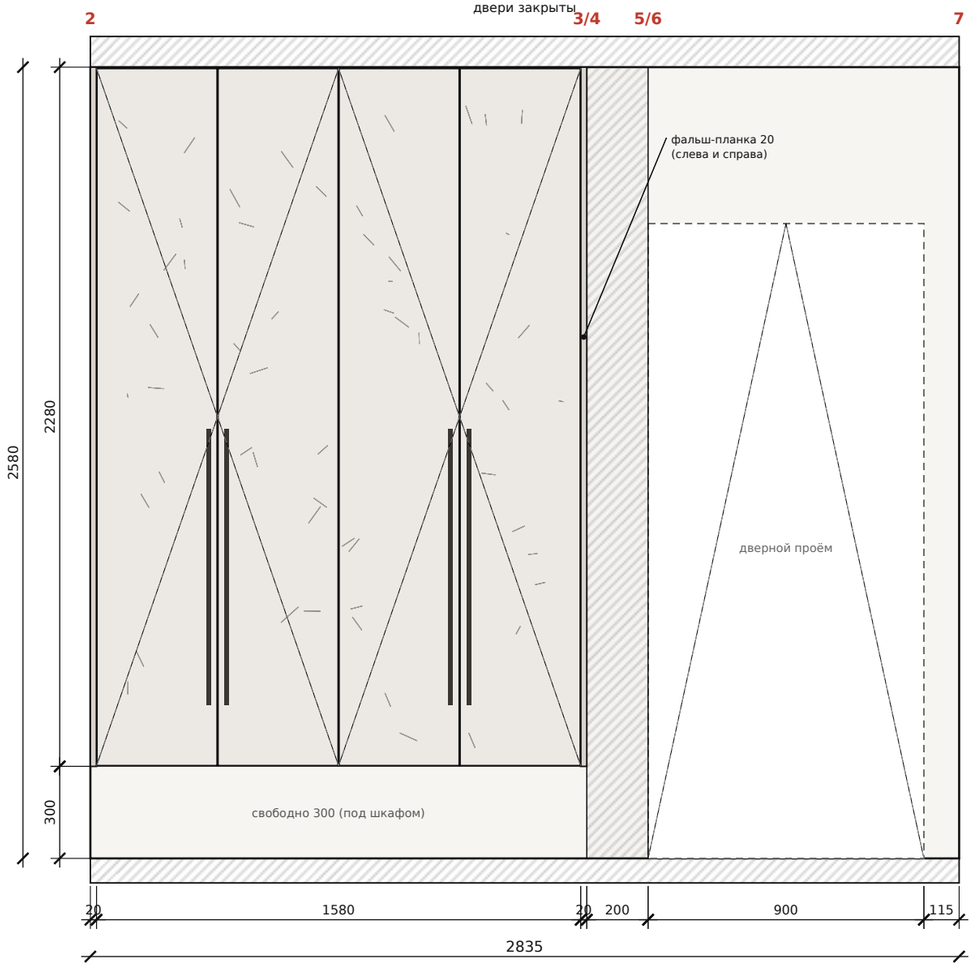


НАПОЛНЕНИЕ

фасады условно сняты

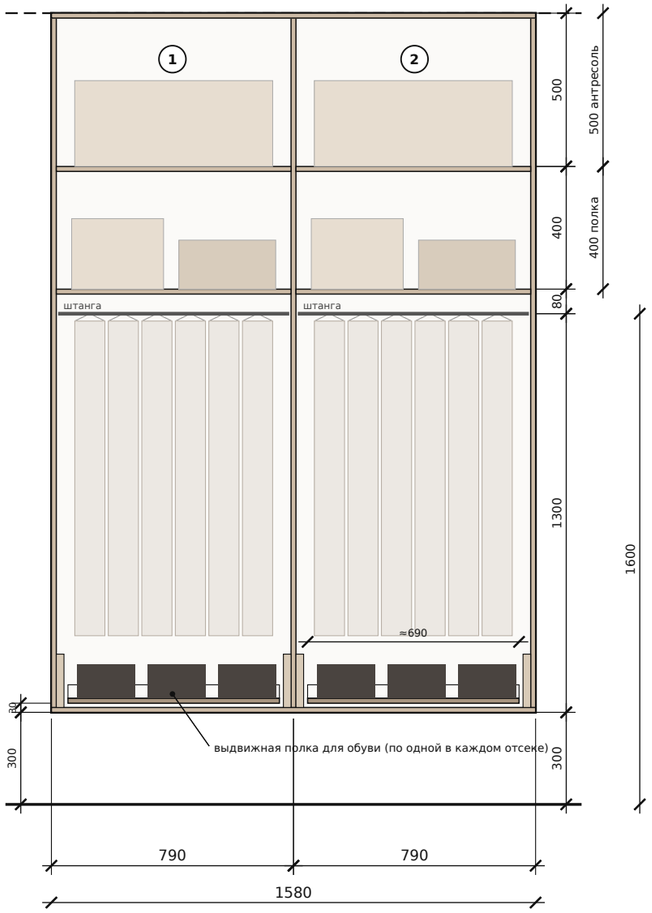


РАЗРЕЗ 1–1

по отсеку 2

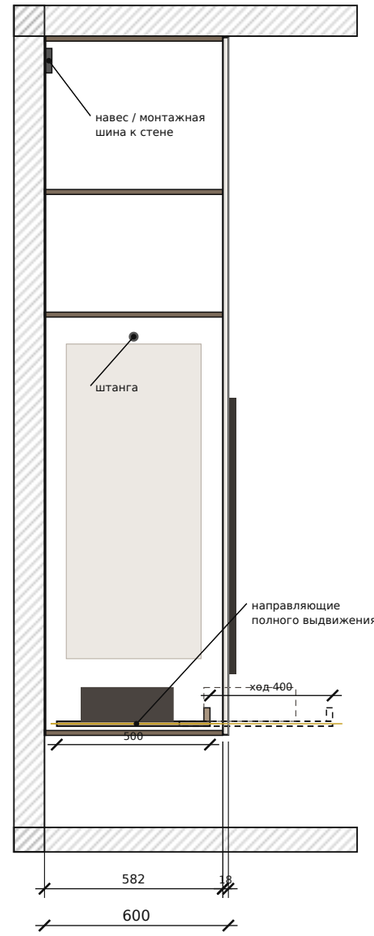

ПЛАН

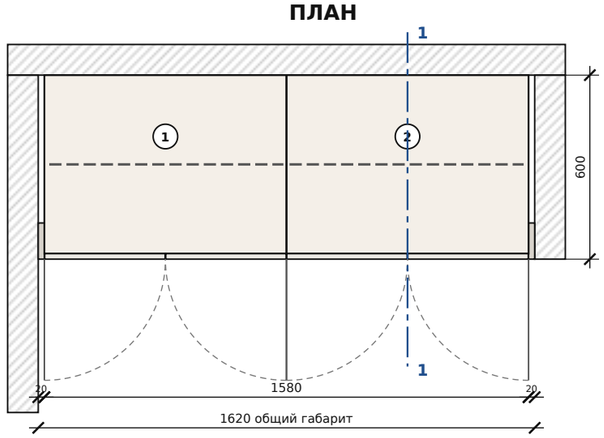

ПРИМЕЧАНИЯ

Шкаф подвесной: низ на 300 мм от чистого пола, верх до потолка (2580).
Корпус 1580 × 600 × 2280 мм; корпус ЛДСП 16, глубина корпуса 582,
фасады 18 мм, 4 распашные двери ≈393 × 2274, по 5 петель на дверь.
Крепление к стене — навесы / монтажная шина, задняя стенка ХДФ.
Отсеки 1 и 2 (по 790): антресоль 500, под ней полка (отделение 400),
штанга на H=1600 (опущена на 400), под штангой ≈1100 до полки обуви.
Внизу в каждом отсеке — выдвижная полка для обуви с бортиком,
направляющие полного выдвижения 500 мм; проставки 25 мм под петли.
Общий габарит 1620 = фальш-планка 20 + корпус 1580 + фальш-планка 20.
Розетки на стене 2–7 (H=250 и H=1950, 200 от края шкафа) попадают
под шкаф и внутрь отсека 2 — уточнить перенос или вырез в задней стенке.
Размеры уточнить по месту после чистовой отделки.

ШКАФ В ПРИХОЖЕЙ

подвесной, стена 2–7

1620 (1580 + 2×20) × 600 × 2280

низ шкафа +300 от пола

Размеры в мм

Масштаб **1:20**

Лист 1 (А3)