

ОБЩИЙ ВИД БЕЗ ФАСАДОВ — НАПОЛНЕНИЕ И РАЗМЕРЫ

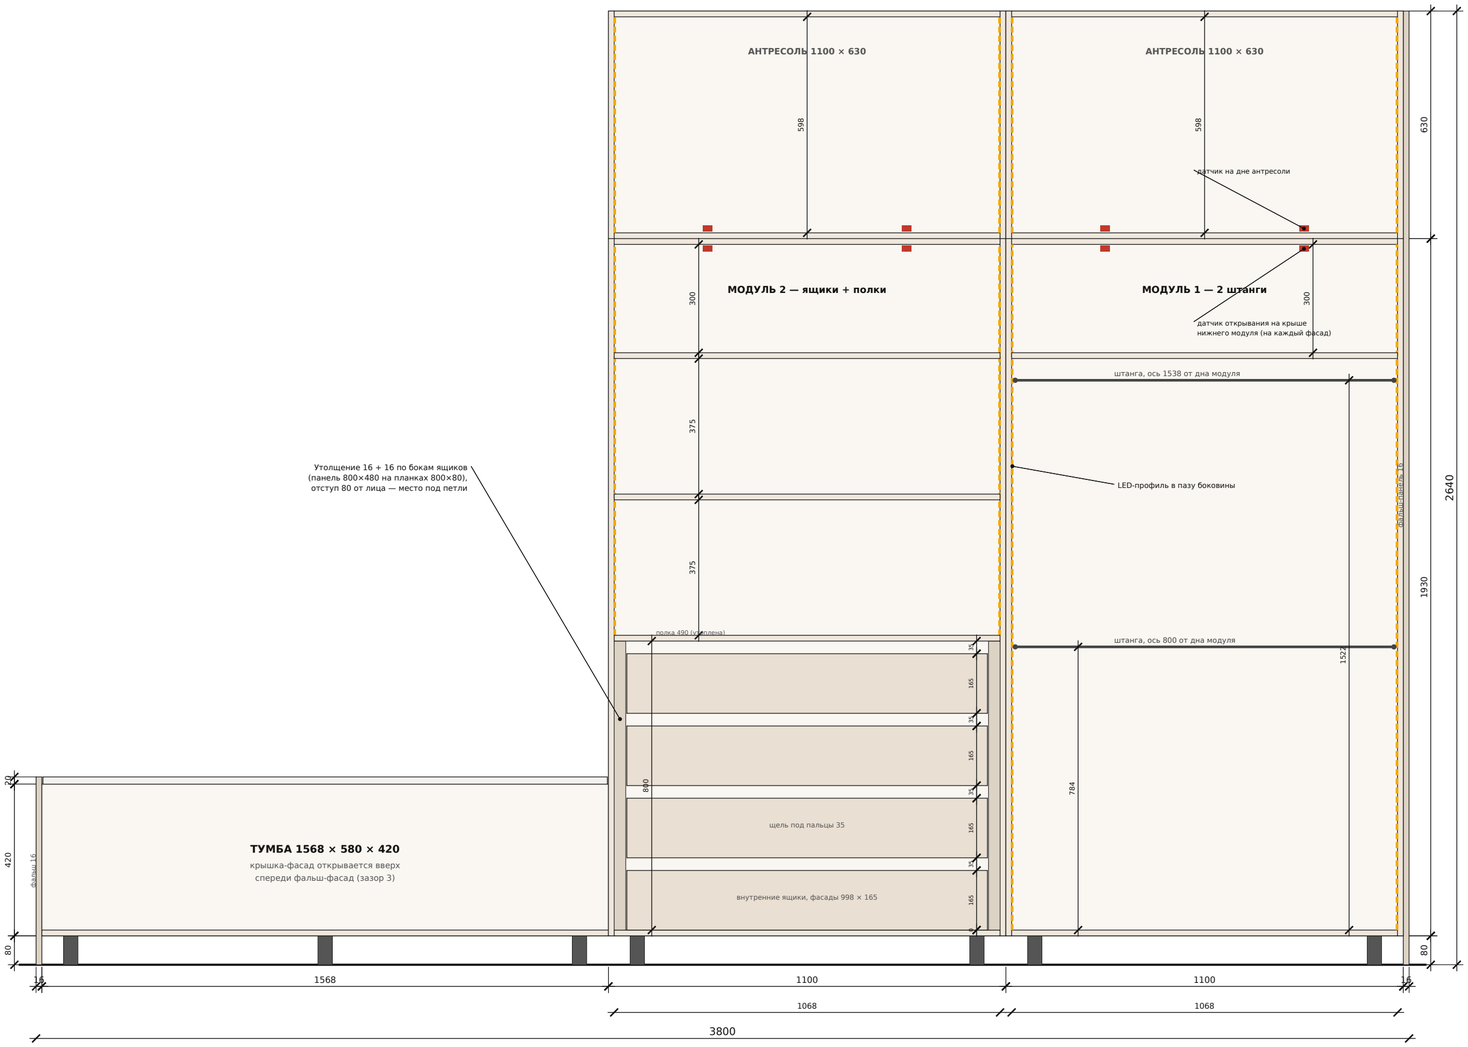


РАЗРЕЗ А–А

по модулю 2, вид слева

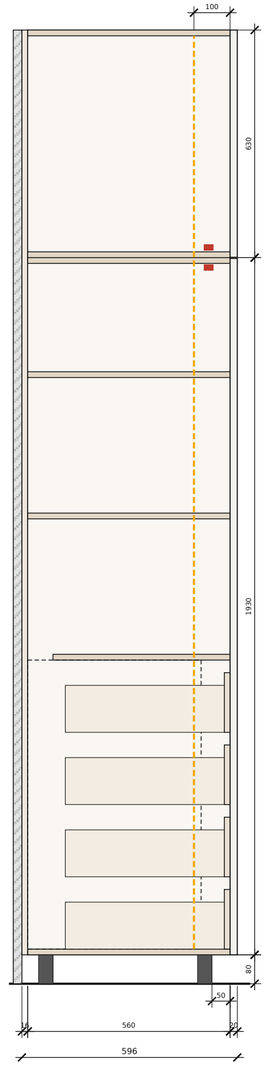

УЗЕЛ Б — ПАЗ ПОД ПОДСВЕТКУ

сечение боковины, вид сверху, М 1:2

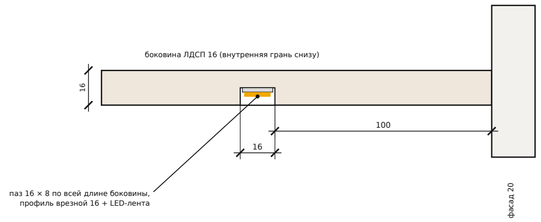

ПРИМЕЧАНИЯ

1. Все размеры полок и ящиков — в свету (между ЛДСП). Отсчёт высот — от низа модуля.
2. Ящики внутренние: 4 шт, фасады 998 × 165, щель под пальцы 35 между фасадами.
3. В модуле с ящиками утолщение по бокам 16 + 16: панель 800×480 на планках 800×80, отступ 80 от лица — ящики не задевают петли фасадов.
4. Подсветка: паз 16 в боковинах по всей длине, 100 от лица; профиль врезной 16 + лента. В модуле 2 лента — выше полки над ящиками.
5. Датчики открывания фасадов: на крыше нижних модулей и на дне антресолей — по 1 на фасад.
6. Ножки 80, отступ 50 от лица корпуса. Фальш-панели 16 по бокам (справа — на всю высоту).
7. Глубина: корпус 560 + задняя ЛДСП 16 + фасад 20 = 596. Левая боковина 580 — до лица фасадов.


ШКАФ С АНТРЕСОЛЬЮ И ТУМБОЙ

Общий вид без фасадов, разрез, паз подсветки

Габариты 3800 × 596 × 2640 Корпус ЛДСП 16, задняя ЛДСП 16	Масштаб **1:12**
Размеры в мм Ножки 80, отступ 50 от лица	Лист **1 (A2)**

ФАСАДЫ — РАЗМЕРЫ, ЗАЗОРЫ 3 мм, ПЕТЛИ

пунктиром за фасадами — полки и ящики (петли не попадают на полки)

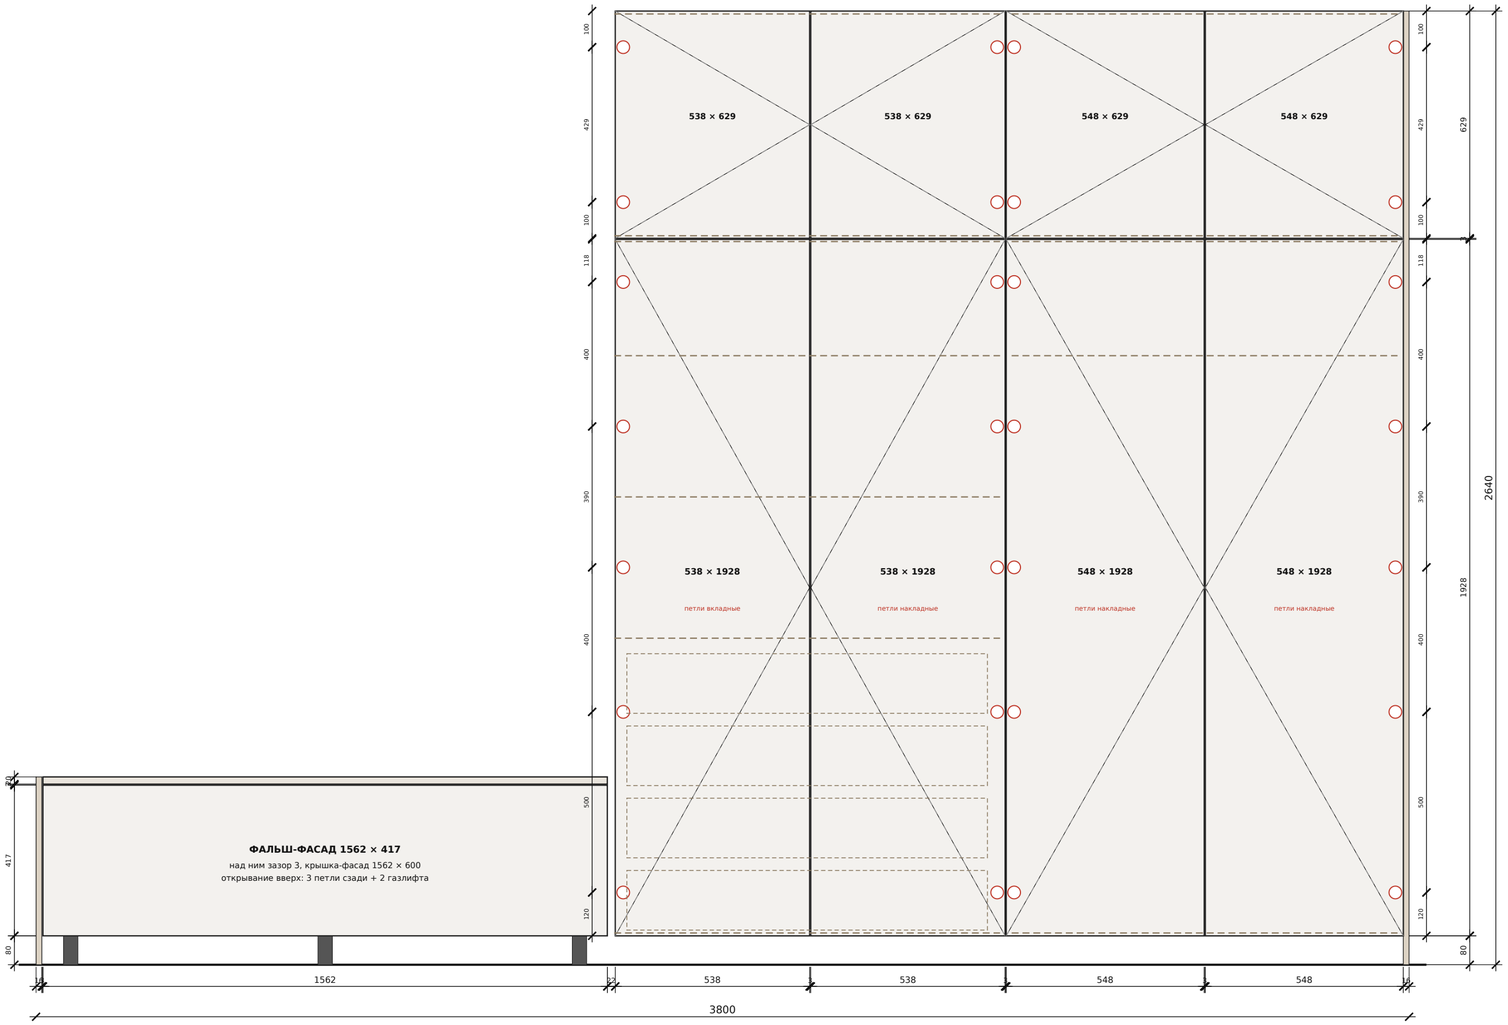

СПЕЦИФИКАЦИЯ ФАСАДОВ

Поз.	Фасад	Размер	Кол.	Петли
Ф1	нижний, левый	538 × 1928	1	вкладные 5
Ф2	нижний	538 × 1928	1	накладные 5
Ф3–Ф4	нижние	548 × 1928	2	накладные 5 + 5
А1	антресоль, левый	538 × 629	1	вкладные 2
А2	антресоль	538 × 629	1	накладные 2
А3–А4	антресоль	548 × 629	2	накладные 2 + 2
Т1	крышка тумбы	1562 × 600	1	3 петли + 2 газлифта
Т2	фальш-фасад тумбы	1562 × 417	1	глухой, на конфирматы/стяжки

ПЕТЛИ — РАССТОЯНИЕ ОТ НИЗА ФАСАДА ДО ОСИ ЧАШКИ

Нижние фасады 1928: 120 · 620 · 1020 · 1410 · 1810

Антресоль 629: 100 · 529

Чашка Ø35, отступ 22 от края фасада (по оси).

Полки (от низа модуля): ящики до 816, полка 816–832; 1207–1223; 1598–1614; крыша 1914.

Ближайшая петля к полке — не ближе 150 мм по оси: 1020 / 1207, 1410 / 1598, 1810 / 1914.

Ф1 и А1 — вкладные петли: левая боковина 580 выступает до лица фасадов.

Открывание: вершина треугольника — сторона открывания, основание — петли.

ШКАФ С АНТРЕСОЛЬЮ И ТУМБОЙ

Фасады: размеры, зазоры, петли

Фасады толщиной 20, зазор 3 Петли — от низа фасада до оси чашки	Масштаб **1:12**
Размеры в мм Полки за фасадами — пунктир	Лист **2 (A2)**

ДЕТАЛИРОВКА — ШКАФ С АНТРЕСОЛЬЮ И ТУМБОЙ

по модулям, в электронном виде

Корпус ЛДСП 16; задние стенки ЛДСП 16 накладные; фасады 20, зазор 3. Размеры — по распилу заказчика; строки с пометкой «+» добавлены. Кромка ПВХ: Д — длина, Ш — ширина; 2 — 2 мм. Паз под LED: 16 × 8 по всей длине боковин, 100 от лица, на внутренней грани.

№	Деталь	Длина	Ширина	Кол.	Кромка	м²	Примечание
Модуль 1 — нижний правый, 2 штанги (1100 × 1930 × 560)							
1	Боковина	1914	560	2	Д1 2	2.14	паз 16 × 8 под LED, 100 от лица (по внутр. грани)
2	Крыша	1100	560	1	Д1 2	0.62	2 отв. под датчики открывания
3	Дно / полка	1068	560	2	Д1 2	1.20	полка: 1598 от низа (300 до крыши)
4	Задняя стенка	1930	1100	1	—	2.12	накладная
Модуль 2 — нижний левый, ящики + полки (1100 × 1930 × 560)							
5	Боковина	1914	560	1	Д1 2	1.07	паз 16 × 8 под LED, 100 от лица (по внутр. грани)
6	Боковина левая (до лица фасадов)	1914	580	1	Д1 2	1.11	паз 16 × 8 под LED, 100 от лица (по внутр. грани); видимая над тумбой
7	Крыша	1100	560	1	Д1 2	0.62	2 отв. под датчики открывания
8	Дно / полки	1068	560	3	Д1 2	1.79	полки: 1207 и 1598 от низа
9	Полка над ящиками	1068	490	1	Д1 2	0.52	816 от низа, утоплена
10	Утолщение: панель	800	480	2	Д1 2	0.77	на планках, отступ 80 от лица
11	Утолщение: планка	800	80	4	—	0.26	16 + 16 по бокам ящиков
12	Ящик: боковина	440	130	8	Д1 2	0.46	
13	Ящик: перед / зад	994	101	8	Д1 2	0.80	
14	Ящик: дно	994	440	4	—	1.75	
15	Ящик: фасад внутренний	998	165	4	Д1 2, Д2 2, Ш1 2, Ш2 2	0.66	щель под пальцы 35
16	Задняя стенка	1930	1084	1	—	2.09	накладная
Антресоли — 2 модуля (1100 × 630 × 560)							
17	Боковина	630	560	3	Д1 2	1.06	паз 16 × 8 под LED, 100 от лица (по внутр. грани)
18	Боковина левая (до лица фасадов)	630	580	1	Д1 2	0.37	паз 16 × 8 под LED, 100 от лица (по внутр. грани)
19	Крыша / дно	1068	560	4	Д1 2	2.39	в днищах — по 2 отв. под датчики
20	Задняя стенка	1100	630	1	—	0.69	накладная
21	Задняя стенка	1084	630	1	—	0.68	накладная

ДЕТАЛИРОВКА — ШКАФ С АНТРЕСОЛЬЮ И ТУМБОЙ

по модулям, в электронном виде

Корпус ЛДСП 16; задние стенки ЛДСП 16 накладные; фасады 20, зазор 3. Размеры — по распилу заказчика; строки с пометкой «+» добавлены. Кромка ПВХ: Д — длина, Ш — ширина; 2 — 2 мм. Паз под LED: 16 × 8 по всей длине боковин, 100 от лица, на внутренней грани.

№	Деталь	Длина	Ширина	Кол.	Кромка	м²	Примечание
Тумба (1568 × 580 × 420)							
22	Перед / зад	1568	404	2	Д1 2	1.27	
23	Бок	548	404	2	—	0.44	
24	Дно	1568	580	1	Д1 2, Д2 2, Ш1 2, Ш2 2	0.91	
Дополнительно (добавлено)							
25	Фальш-панель правая, на всю высоту **+**	2640	596	1	Д1 2, Ш1 2	1.57	в цвет фасадов/корпуса
26	Фальш-панель левая (у тумбы) **+**	520	600	1	Д1 2, Ш1 2	0.31	
Фасады 20 (зазор 3)							
27	Фасад нижний Ф1 (петли вкладные) **+**	1928	538	1	—	1.04	петли: 120, 620, 1020, 1410, 1810
28	Фасад нижний Ф2 **+**	1928	538	1	—	1.04	петли: 120, 620, 1020, 1410, 1810
29	Фасад нижний Ф3, Ф4 **+**	1928	548	2	—	2.11	петли: 120, 620, 1020, 1410, 1810
30	Фасад антресоли А1 (петли вкладные) **+**	629	538	1	—	0.34	петли: 100, 529
31	Фасад антресоли А2 **+**	629	538	1	—	0.34	петли: 100, 529
32	Фасад антресоли А3, А4 **+**	629	548	2	—	0.69	петли: 100, 529
33	Крышка тумбы (фасад, вверх) **+**	1562	600	1	—	0.94	3 петли сзади + 2 газлифта
34	Фальш-фасад тумбы **+**	1562	417	1	—	0.65	зазор 3 до крышки

Материал	Площадь (без запаса)	Кромка 2 мм
ЛДСП 16	**27.68 м²**	**57.2 м**
Фасад 20	**7.14 м²**	**0.0 м**

ФУРНИТУРА — ШКАФ С АНТРЕСОЛЬЮ И ТУМБОЙ

петли, ящики, подсветка, крепёж

Наименование	Кол.	Где / примечание
Петли (с доводчиком)		
Петля накладная 110° с доводчиком	21	Ф2–Ф4 по 5, А2–А4 по 2
Петля вкладная 110° с доводчиком	7	Ф1 — 5, А1 — 2 (левая боковина выступает)
Монтажная планка	28	
Петля для крышки тумбы (мебельная, откидная)	3	крышка 1562 × 600
Газлифт / подъёмник крышки	2	подобрать по весу крышки
Ящики и наполнение		
Направляющие шариковые полного выдвижения, пара	4	под коробку 440 (L 400–450 по каталогу)
Штанга овальная, L 1066	2	модуль 1, оси 1538 и 800 от низа
Штангодержатель	4	
Подсветка		
Профиль алюм. врезной 16 + рассеиватель, всего 8.4 м	1	модуль 1: 2 × 1898; модуль 2: 2 × 1082; антресоли: 4 × 598
Лента LED 24 В, м	10	с запасом 10 %
Датчик открывания двери (на подсветку)	8	на каждый фасад: крыша нижних модулей, дно антресолей
Блок питания 24 В, 100 Вт	1	
Провод, коннекторы, распределитель	1	комплект
Крепёж и монтаж		
Ножка регулируемая 80 мм	14	нижние модули 2 × 4, тумба 6; отступ 50 от лица
Конфирмат 7 × 50	160	с запасом
Заглушка конфирмата	40	видимые места
Саморез 4 × 30 (задние стенки ЛДСП 16)	120	
Стяжка межсекционная	12	модули между собой и антресоли к нижним
Крепление к стене (уголок/навес)	6	