

ФАСАД — СТЕНА 25–26

двери закрыты, стол в торец

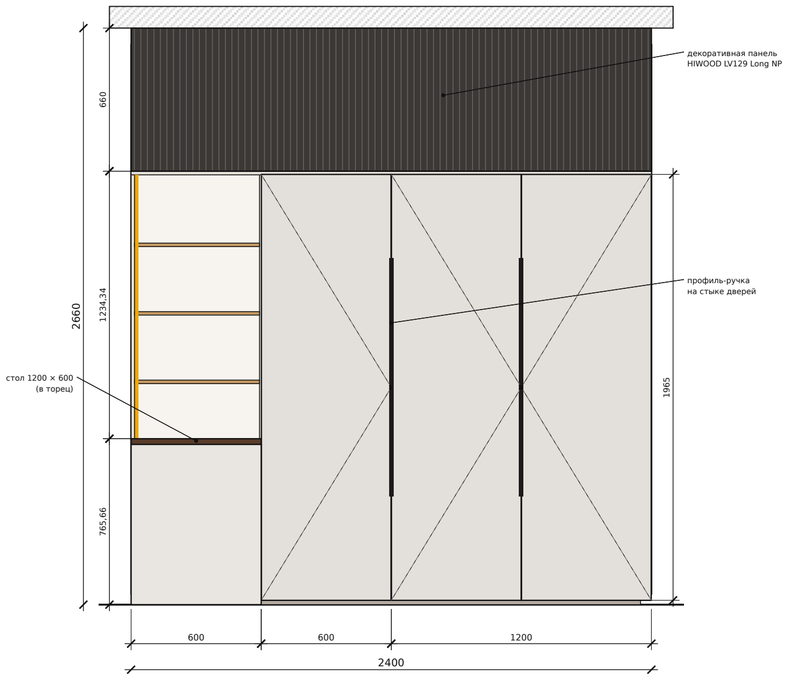


НАПОЛНЕНИЕ

двери, панель и стол условно сняты

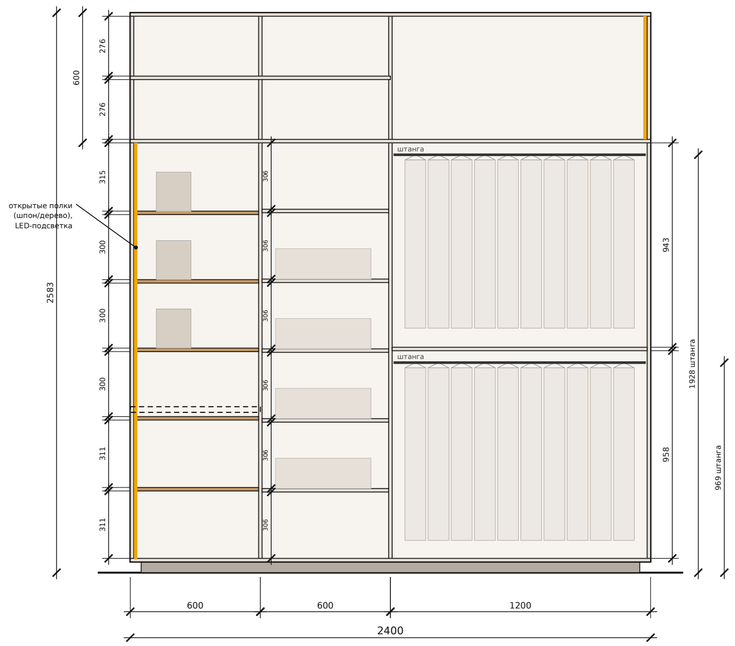


ВИД СБОКУ — СТОЛ

столешница выходит из шкафа, тумба с ящиками

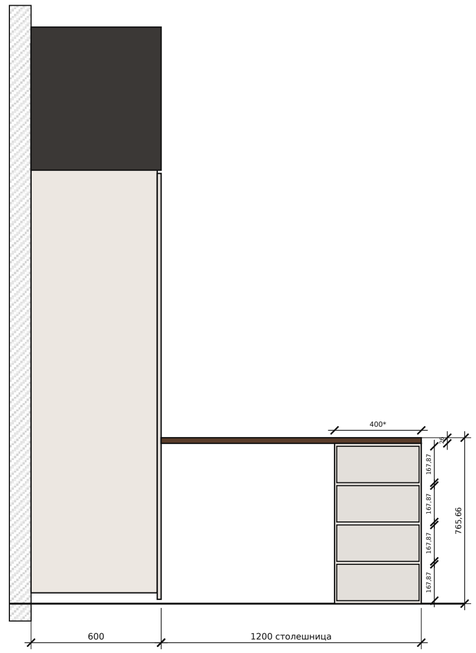

ПЛАН

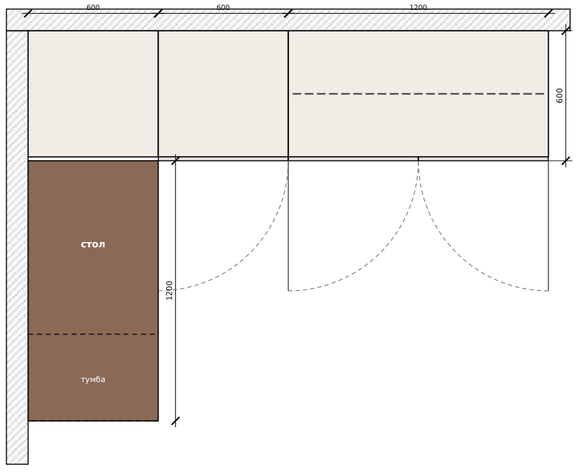

ПРИМЕЧАНИЯ

Шкаф 2400 × 600 × 2583, цоколь 50; над ним декоративная рейчатая панель HIWOOD LV129 Long NP высотой 660 по всей ширине (до потолка 2660).
Секции: 600 открытые полки с LED (снизу 311 / 311, выше 300 × 3 и 315), 600 полки за дверью (≈306), 1200 две штанги (зоны 958 / ≈902).
Антресоль 600: два отделения по 276, справа — с вертикальной подсветкой.
Двери: 3 распашные по 600, высота 1965, профиль-ручка на стыках.
Стол: столешница 1200 × 600 × 26 (орех), высота 765,66, выходит из шкафа в торец левой секции; тумба 4 ящика по 167,87 (ширина 400* — принято).
Материалы фасадов/корпуса уточнить; фасады показаны в светлом камне.
Размеры уточнить по месту.

ШКАФ СО СТОЛОМ

стена 25–26, по эскизам заказчика

шкаф 2400 × 600 × 2583, стол 1200 × 600

панель HIWOOD LV129, столешница орех

Размеры в мм

Масштаб **1:20**

Лист 1 (А2)