

РАЗВЁРТКА СТЕНЫ 10–9

кухня, вид из комнаты

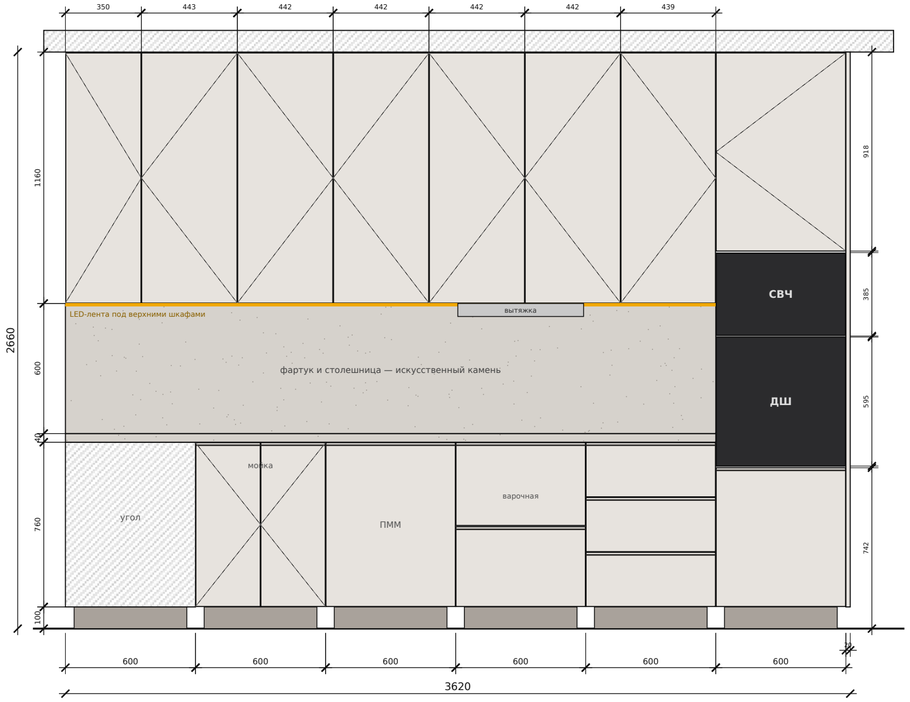


РАЗВЁРТКА СТЕНЫ 10–11/12

угловой ряд и холодильник

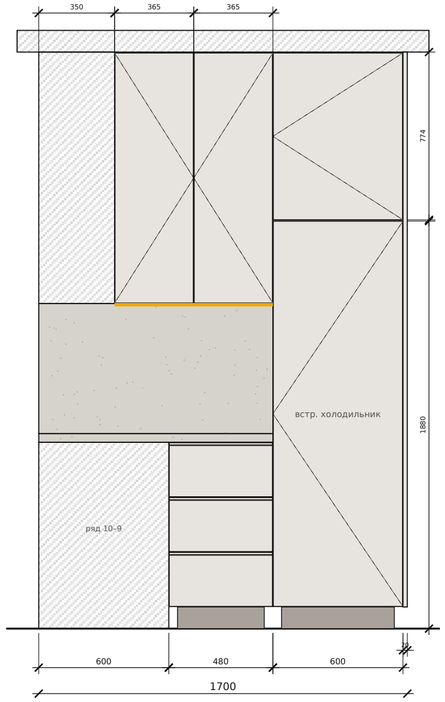


ОСТРОВ

вид со стороны кухни и разрез

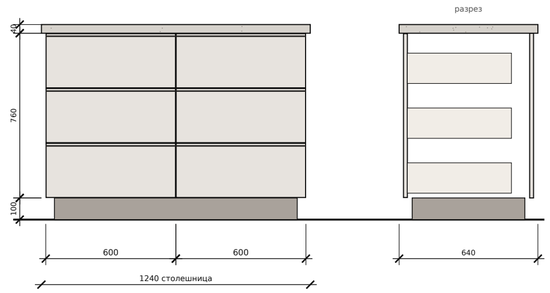

ПЛАН КУХНИ

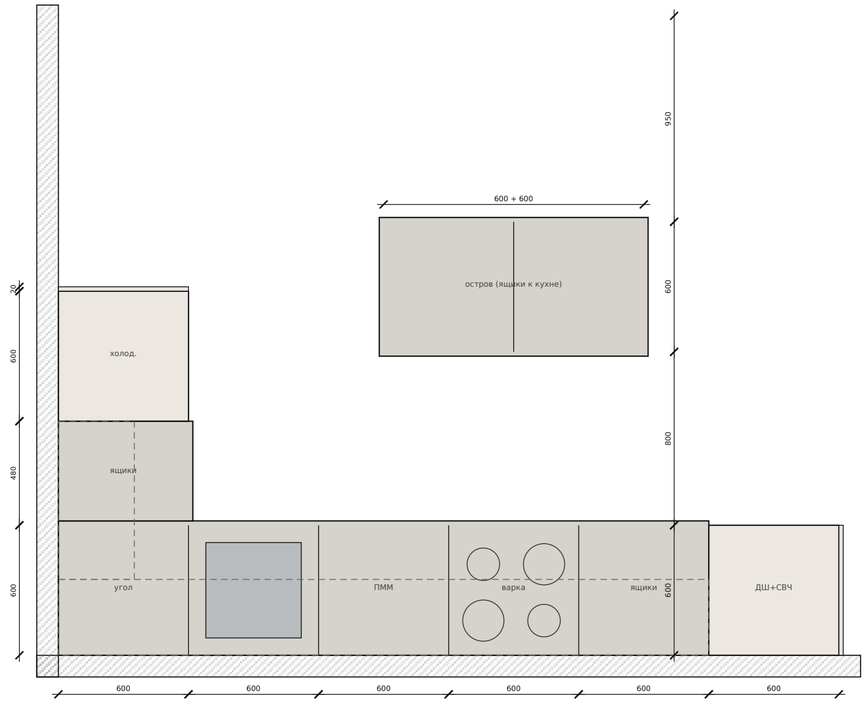

ПРИМЕЧАНИЯ

Нижние модули: цоколь 100, корпус до 860, столешница искусственный камень 40 (верх 900).

Фартук — искусственный камень, высота 600; верхние шкафы 1160 — до потолка (2660), глубина 350.

Ряд стены 10–9 (слева направо от угла): глухой угол (проточный водонагреватель), мойка, ПММ 60, варочная панель (2 ящика), 3 ящика, пенал 600: ящик, духовой шкаф, СВЧ, дверца.

Ряд стены 10–11/12: ящики 480, пенал встроенного холодильника 600 + фальш-панель 20.

Верхние шкафы: 350 / 443 / 442 / 442 / 442 / 442 / 439 и 365 / 365; LED-лента под шкафами.

Вытяжка встроенная под шкаф над варочной панелью, выдвижной козырёк.

Остров 2 × 600 × 600, ящики со стороны кухни; 800 от кухни, 950 до стены 13–14.

Фасады — под камень (как в проекте), открывание через профиль (gola) / push-to-open.

Размеры мебели условные по дизайн-проекту — уточнить по замеру и технике.

КУХНЯ С ОСТРОВОМ

кухня-гостиная, стены 10–9 и 10–11/12

3600 + 1700, остров 1200 × 600

ДШ, СВЧ, ПММ, холодильник, варка

Размеры в мм

Масштаб **1:20**

Лист 1 (А2)