

ФАСАД

фасады закрыты

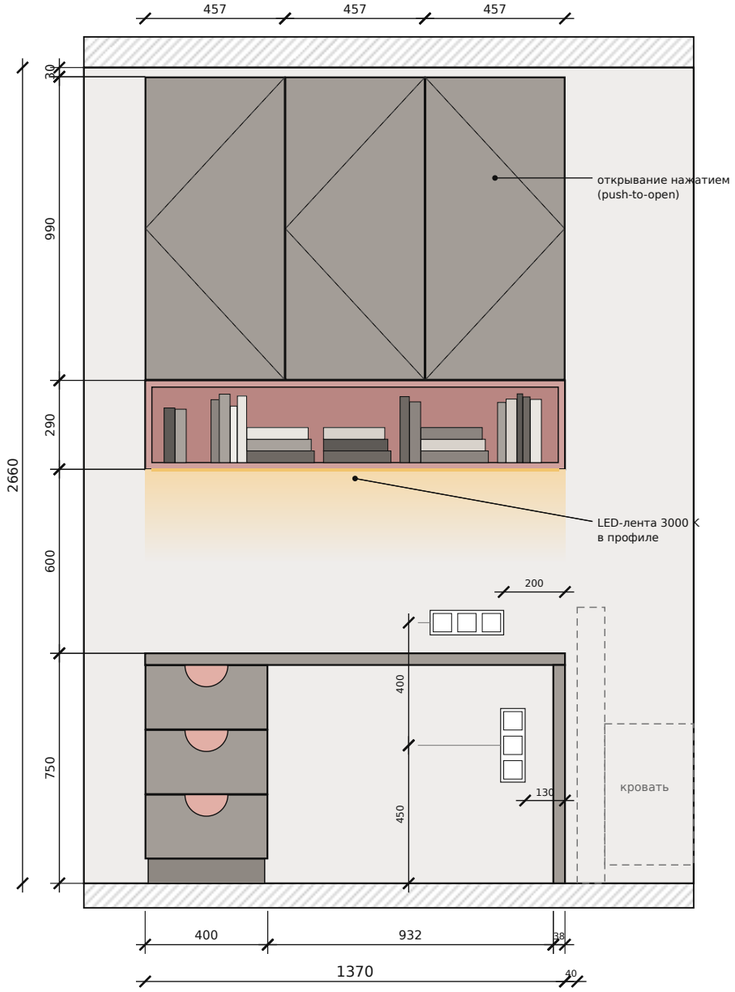


НАПОЛНЕНИЕ

фасады условно сняты

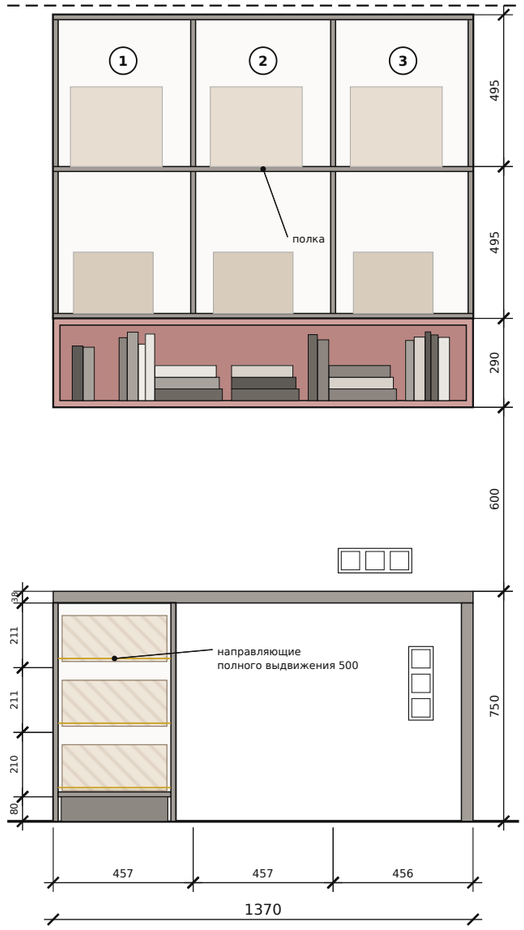


РАЗРЕЗ 1–1

через тумбу

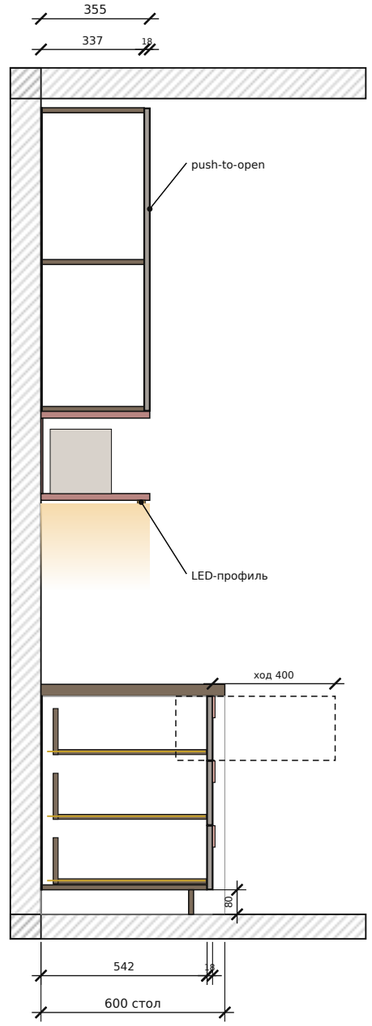

ПЛАН

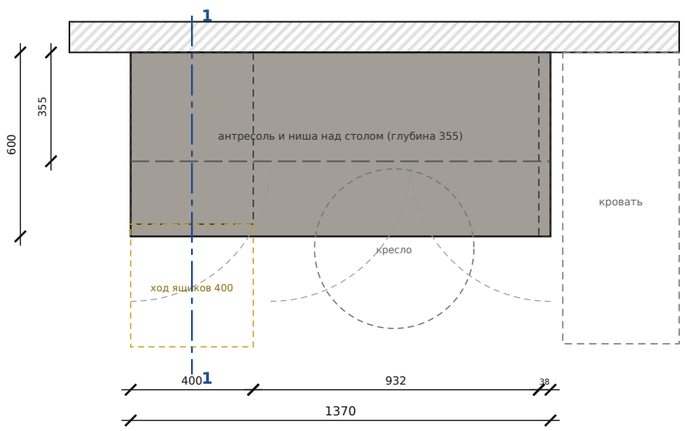

ПРИМЕЧАНИЯ

Общая ширина 1370; высота помещения принята 2660 (750 + 600 + 1310), уточнить по месту.
Антресоль 1370 × 990 × 355: корпус ЛДСП 16, 3 фасада МДФ 18 ≈455 × 986,
открывание нажатием (push-to-open), в каждом отсеке полка на H=2135. Зазор 30 до потолка.
Открытая ниша 1370 × 290 × 355, ЛДСП 22 «пыльная роза», задняя стенка в цвет;
снизу LED-лента 3000 K в профиле, длина ≈1330.
Стол: столешница 1370 × 600 × 38, справа опора 38 × 712 × 600 (соединение на 45° или стяжки).
Тумба 400 × 712 × 560: цоколь 80 (утоплен на 60), 3 ящика 210 / 211 / 211,
направляющие полного выдвижения 500; ручки — полукруг Ø140, розовые.
Розетки: над столом 2 шт. + выключатель (центр H=850, 200 от правого края),
под столом интернет + 2 шт. (центр H=450, 130 от правого края).
Цвета: серо-бежевый #8E8882 (фасады, стол), ниша #C4908C, ручки #E2AFA6.
Глубины на исходном эскизе не указаны — приняты 355 / 600 / 560.

РАБОЧЕЕ МЕСТО В ДЕТСКОЙ

антресоль, ниша с подсветкой, стол с тумбой

1370 × 600 × 2630

стол H=750, цоколь тумбы 80

Размеры в мм

Масштаб

1:20

Лист 1 (А3)