
Металлический каркас домика — план (вид сверху)

Труба профильная 80×80 — обвязки, стойки, перемычки, перегородки | Высота 3000 | Шаг стоек ≤ 2000 | Размеры в мм, 1:50

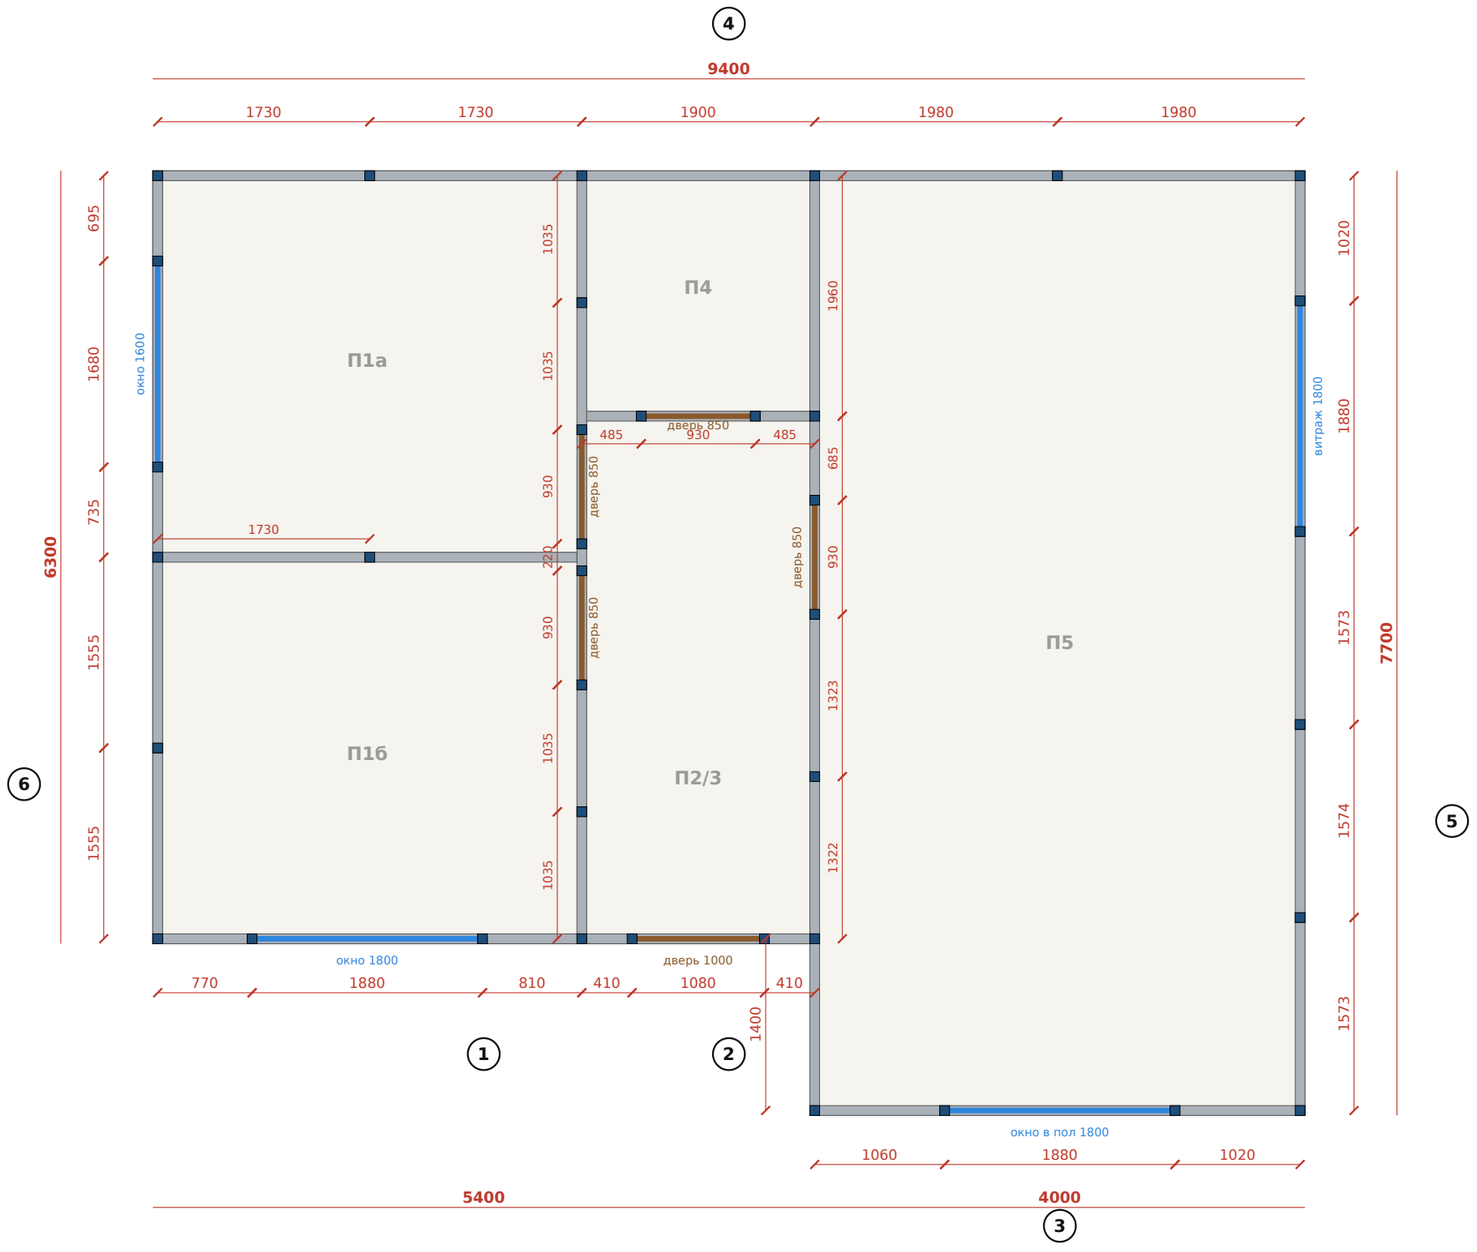

Условные обозначения

- Стойка 80×80, h = 2840 (между обвязками)
- Обвязка 80×80 (верхняя; нижняя — под ней)
- Окно / витраж: перемычка сверху, ригель снизу
- Дверь: перемычка сверху, нижняя обвязка разрезана

Решения по каркасу


1. Всё из трубы 80×80 (стенка 3 мм), сварка.
2. Наружные стены — труба внутрь от наружной грани; внутренние перегородки — по осям.
3. Нижняя и верхняя обвязка — по всем стенам и перегородкам; в дверных проёмах нижняя обвязка вырезается (порог).
4. Стойки: в углах, на примыканиях перегородок, по обе стороны каждого проёма и промежуточные с шагом не более 2000 мм (размеры — по осям).
5. Над каждым проёмом — перемычка 80×80, под окнами (низ 900) — подоконный ригель.
6. Примыкания рядом с дверью (П1а/П1б, П4) опираются на стойки проёма — отдельная стойка не ставится, чтобы не было зазора 30 мм между трубами.
7. Стыки обвязок — встык с проваркой; пролёты 9400 и 7540 — из хлыста 12 м.
8. Крыша, раскосы, закладные и анкеры — по отдельному расчёту.

Стоек: 38 шт. · Трубы всего: 221.0 м


Спецификация и раскрой — лист 2

Металлический каркас домика — 3D и спецификация

Труба профильная 80×80×3 | Цвета: обвязки — серые, стойки — синие, перемычки — оранжевые, подоконные ригели — зелёные

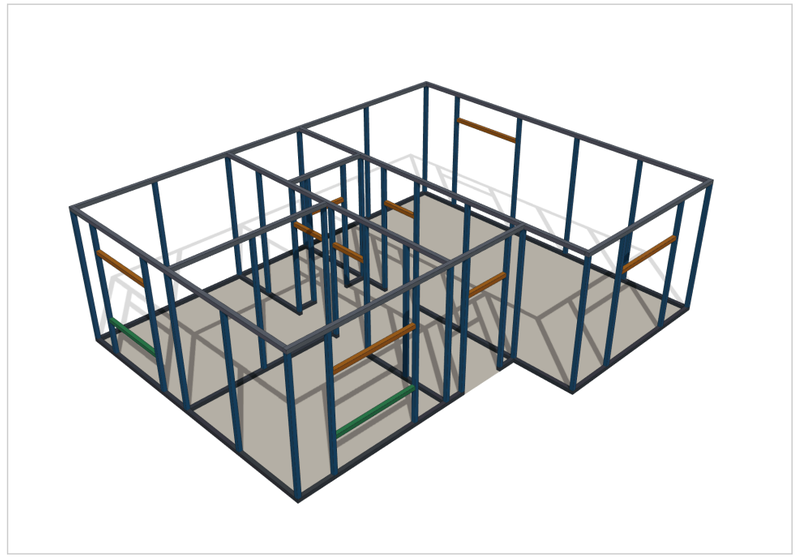


Вид с юго-запада (стены 1, 2, 3, 6)

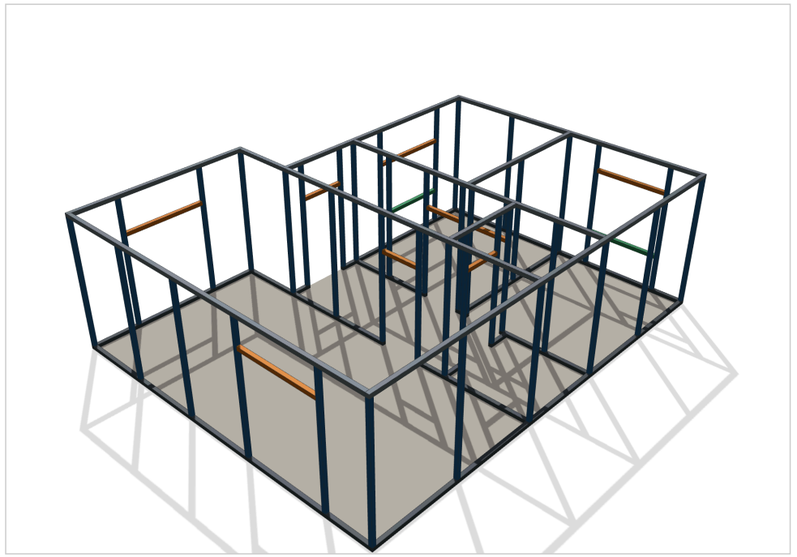

Вид с северо-востока (стены 4, 5)

Раскрой на хлысты 12 м (пропил 3 мм)

Хлыстов: 20 шт. = 240 м, отход 19.0 м (8%)

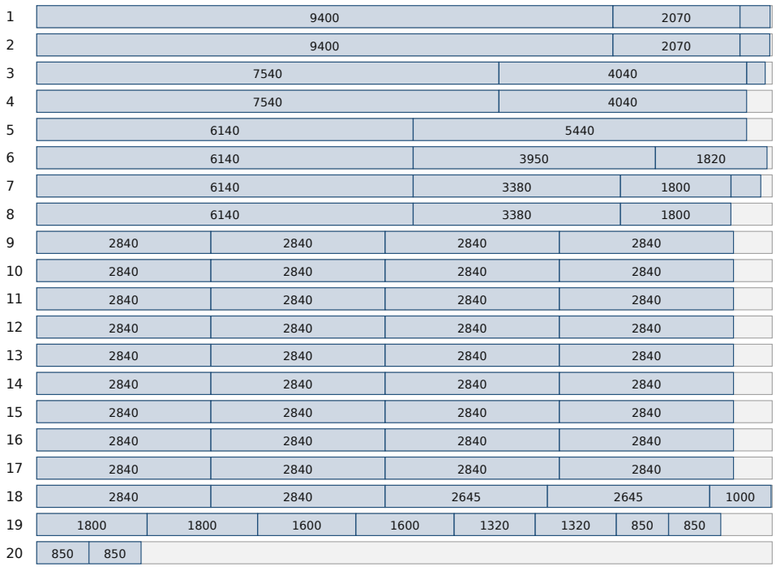

Спецификация (длины по факту реза)

№	Элемент	Длина, мм	Кол-во	Всего, м	Масса, кг
1	нижняя обвязка	9400	1	9.40	66.5
2	нижняя обвязка	7540	1	7.54	53.3
3	нижняя обвязка	6140	1	6.14	43.4
4	нижняя обвязка	4040	1	4.04	28.6
5	нижняя обвязка	3950	1	3.95	27.9
6	нижняя обвязка	3380	1	3.38	23.9
7	нижняя обвязка	2645	2	5.29	37.4
8	нижняя обвязка	2070	2	4.14	29.3
9	нижняя обвязка	1320	1	1.32	9.3
10	нижняя обвязка	490	1	0.49	3.5
11	нижняя обвязка	485	2	0.97	6.9
12	нижняя обвязка	300	1	0.30	2.1
13	верхняя обвязка	9400	1	9.40	66.5
14	верхняя обвязка	7540	1	7.54	53.3
15	верхняя обвязка	6140	3	18.42	130.2
16	верхняя обвязка	5440	1	5.44	38.5
17	верхняя обвязка	4040	1	4.04	28.6
18	верхняя обвязка	3380	1	3.38	23.9
19	верхняя обвязка	1820	1	1.82	12.9
20	верхняя обвязка	1320	1	1.32	9.3
21	стойка	2840	38	107.92	763.0
22	перемычка	1800	3	5.40	38.2
23	перемычка	1600	1	1.60	11.3
24	перемычка	1000	1	1.00	7.1
25	перемычка	850	4	3.40	24.0
26	подоконный ригель	1800	1	1.80	12.7
27	подоконный ригель	1600	1	1.60	11.3
	ИТОГО		**74**	**221.0**	**≈ 1563**

Примечания

• Масса: 7.07 кг/м для 80×80×3 (ГОСТ 30245); при стенке 4 мм — ≈ 9,2 кг/м, масса вырастет примерно на 30%.
• Длинные обвязки 9400 и 7540 — цельными из хлыста 12 м; если хлысты 6 м — стык со вставкой-накладкой над стойкой.
• Запас на брак и подгонку — +5% к закупке.
• Раскосы жёсткости в углах и кровля в расчёт не входят.