

ФАСАД

тумба, шкаф, фальш-планки 20

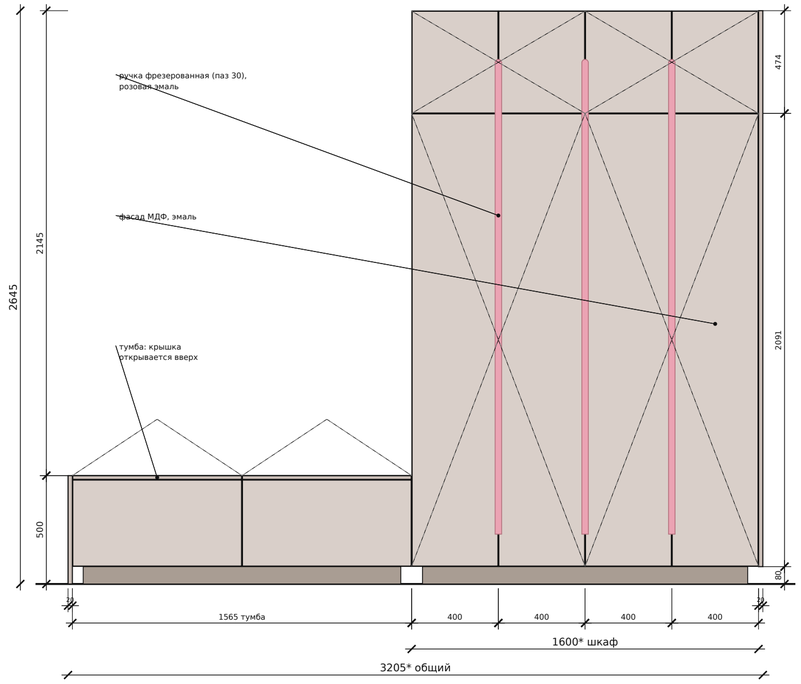


НАПОЛНЕНИЕ

фасады условно сняты

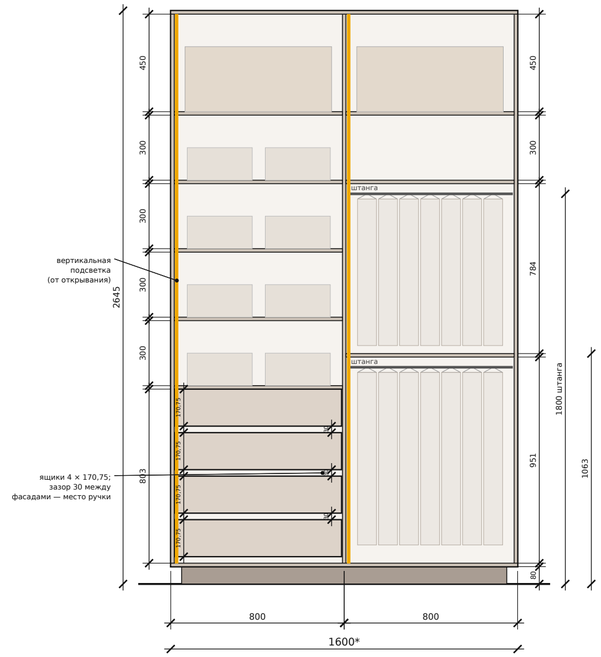


РАЗРЕЗ 1–1

по отсеку с ящиками

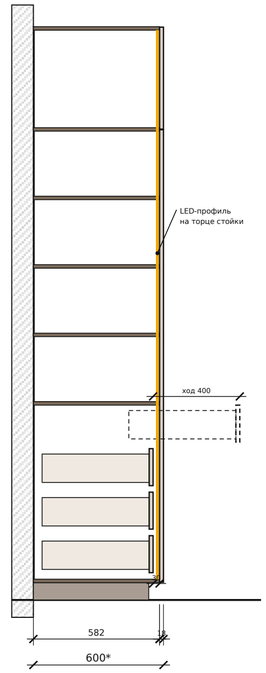


ТУМБА — РАЗРЕЗ 2–2

крышка открывается вверх

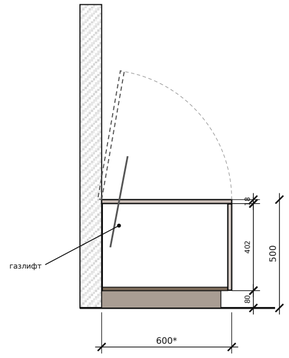

ПЛАН

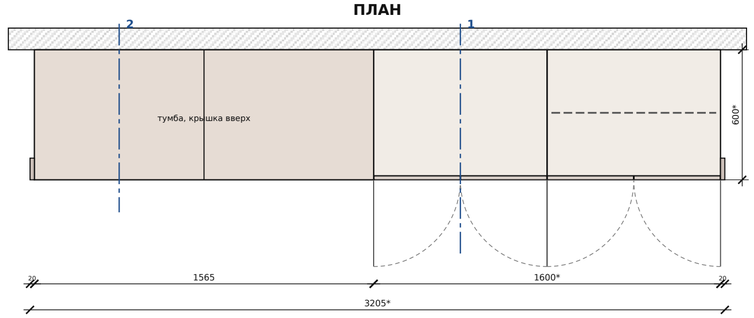

ПРИМЕЧАНИЯ

Корпус — ЛДСП Egger 16 мм, цвет «Кашемир»; цоколь 80.
Фасады — МДФ 18 мм, эмаль; 4 нижние + 4 антресольные двери, зазор 3 мм.
Ручка фрезерованная: паз 30 мм на стыках створок, розовая эмаль, верх скруглён.
Левый отсек: антресоль 450, 4 полки с шагом 300, блок ящиков 803:
4 внутренних ящика, фасады 170,75, зазор между ними 30 — место ручки;
отступ 30 от края, направляющие полного выдвижения 500 мм.
Правый отсек: антресоль 450, полка 300, штанга H=1800 (зона 784),
полка, нижняя штанга H=1000 (зона 951).
Вертикальная LED-подсветка в каждом отсеке, включение от открывания.
Тумба слева: 1565 × 500 (без фальш-планки), крышка открывается вверх
на газлифтах, петли у стены; цоколь 80.
Фальш-планки 20 мм: слева у тумбы (H=500) и справа у шкафа (во всю высоту).
* Ширина шкафа 1600 и глубина 600 (шкаф и тумба) не указаны — ПРИНЯТЫ, уточнить.
Размеры в свету между полками — как на эскизе заказчика.

ШКАФ С ЯЩИКАМИ И ТУМБА

по эскизу заказчика

шкаф 1600* × 600* × 2645, тумба 1565 × 500	Масштаб **1:20**
ЛДСП Egger «Кашемир», МДФ эмаль	
Размеры в мм	Лист 1 (А2)